


			ADNOC GAS HABSHAN & BAB CONTROL SYSTEMS UPGRADE (PACKAGE 1) PROJECT NO. 0405323						TARGET 				
			COMMENTS RESOLUTION SHEET										
Document Title:			PIPING & INSTRUMENTATION DIAGRAM CLOSED DRAIN & UTILITY SYSTEM THAMMAMA 'B' & 'C'			AGP Response Code			Prepared By:	VK			
Document No:			22-00-307		Revision No:	B	1. Revise and Re-submit		3. Approved	X	Checked By:	DV	
AG Ref. No:			ADNOCGP-WTRAN-007987		Date:	20-Jun-2024	2. Approved with comments		4. For Information only		Approved By:	YVR	
SN	Reference		COMPANY Comments				CONSULTANT Response			COMPANY Resolution			
	Page No.	Clause No.											
1	1	Process Comment	Please note that earlier revision A existing scope is not considered				Updated based on piping input after recent site survey.						

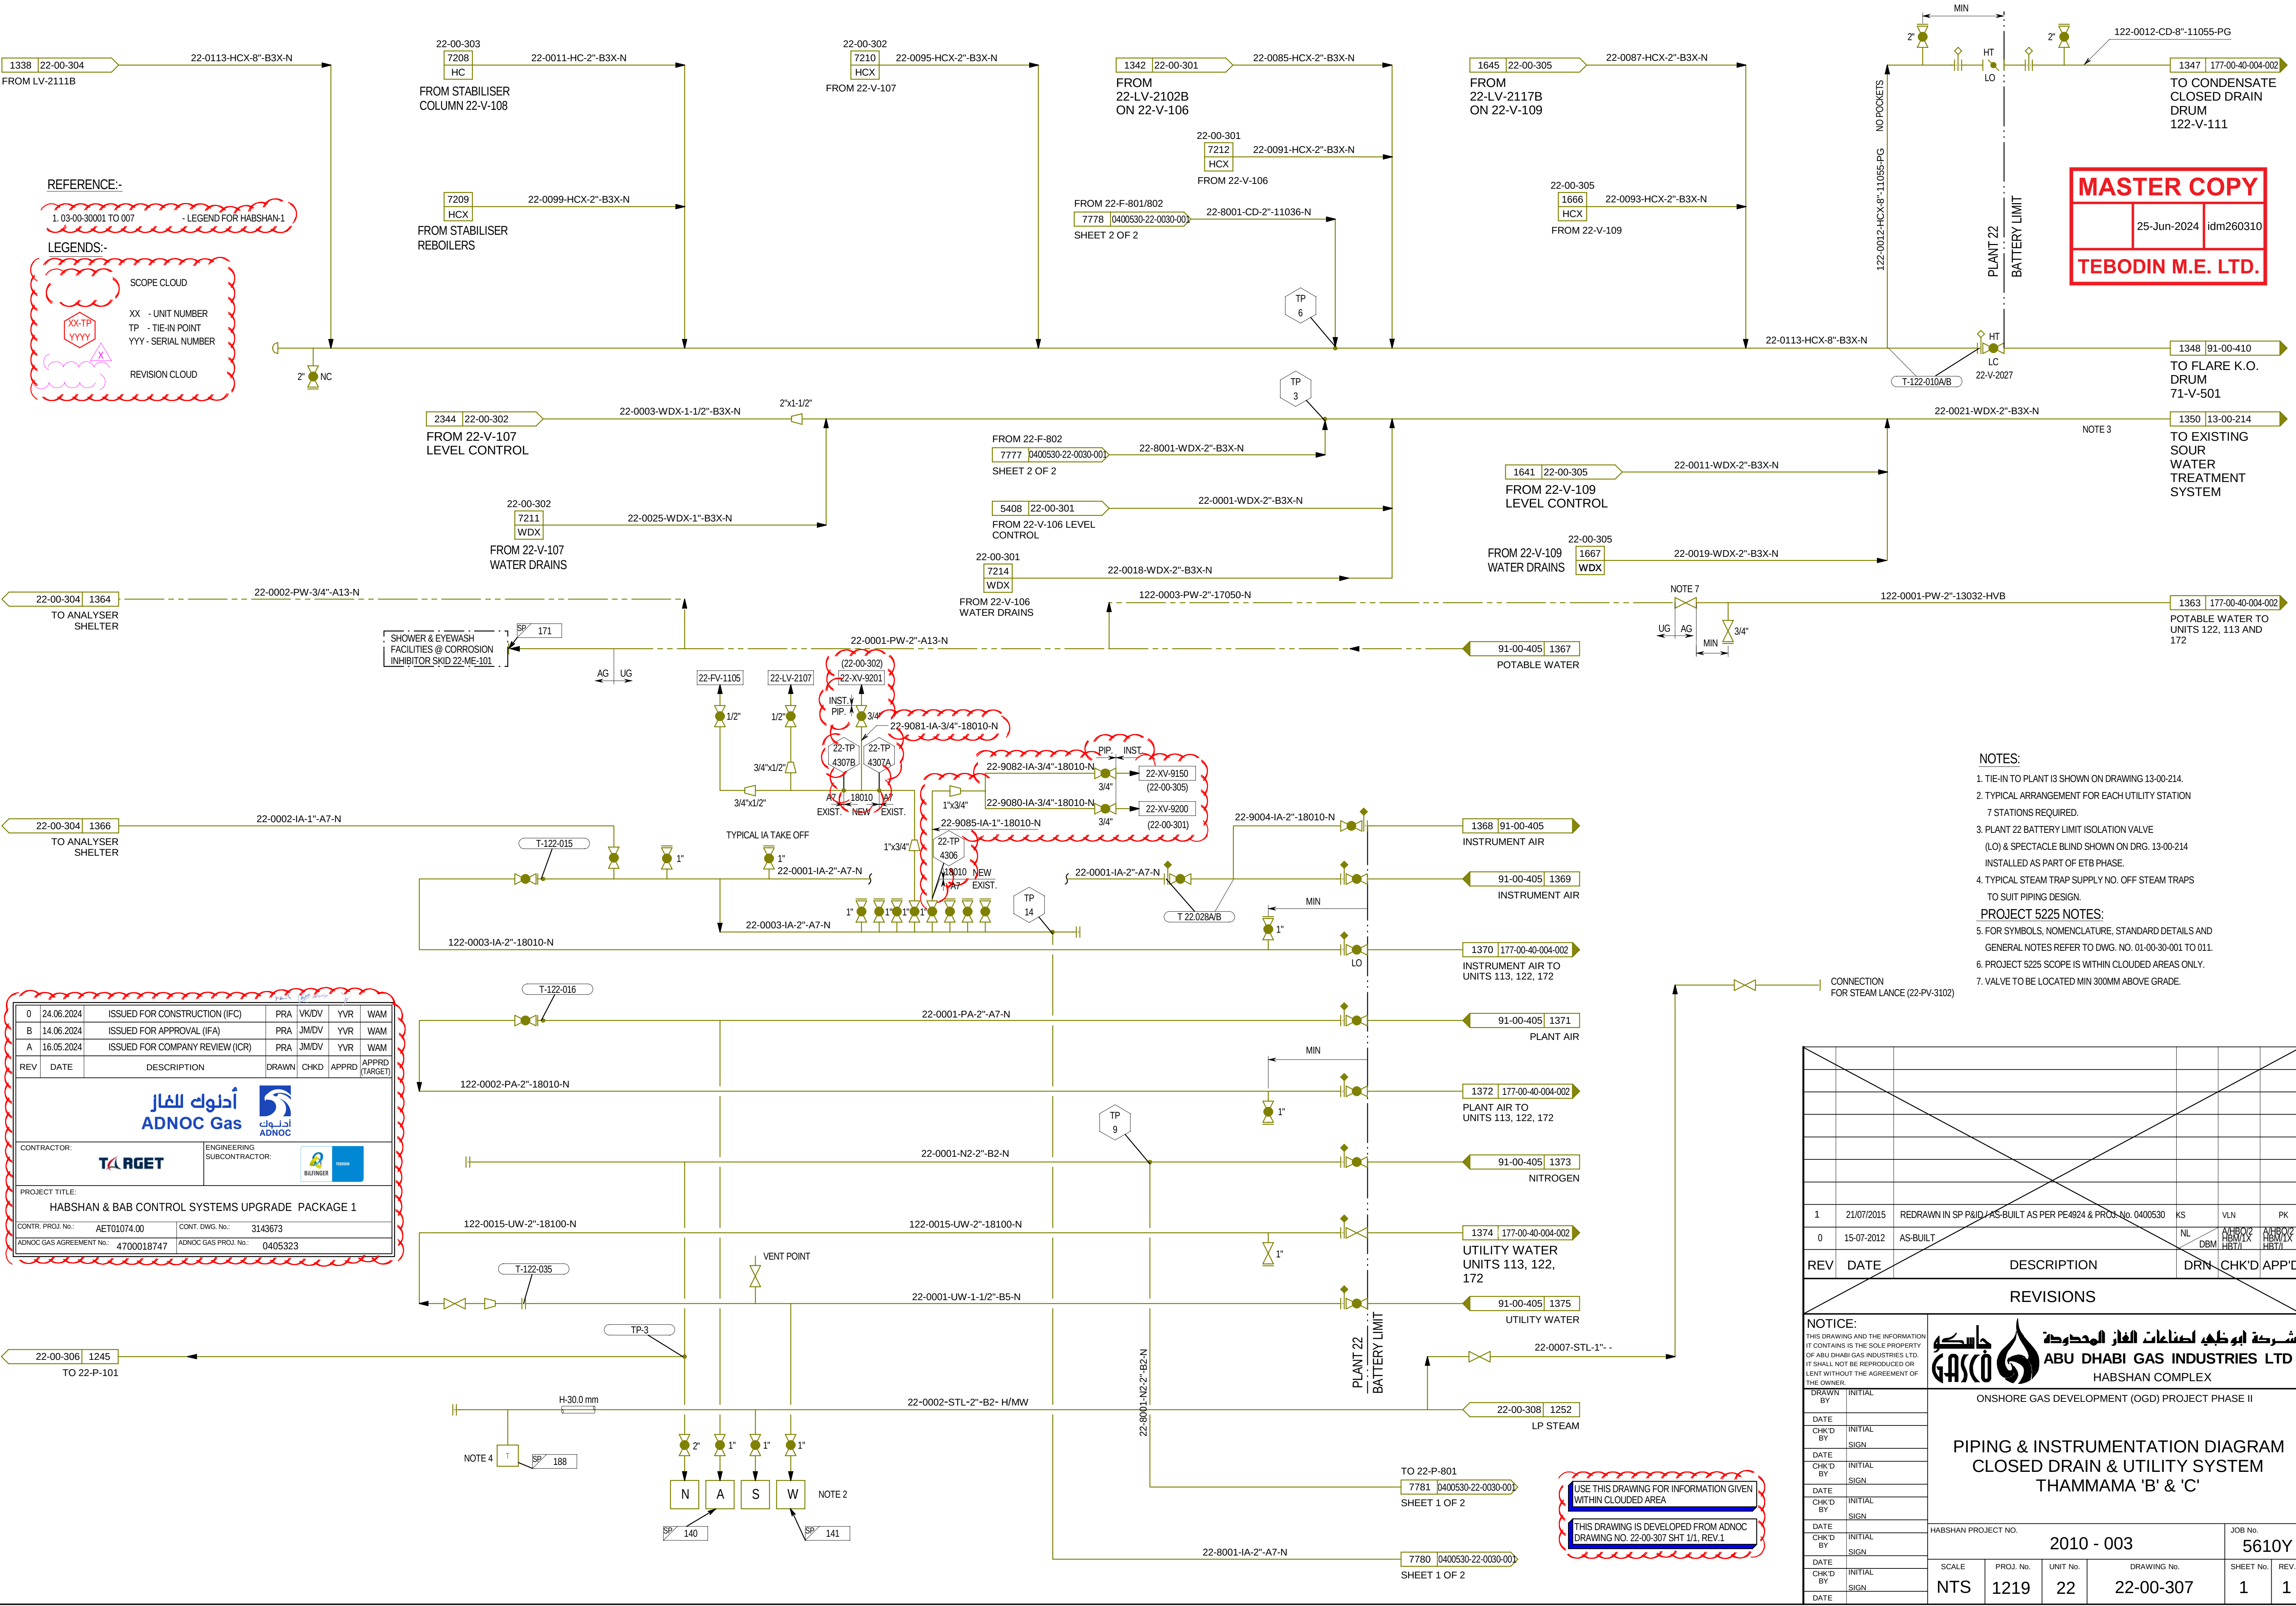

MASTER COPY

25-Jun-2024 idm260310

TEBODIN M.E. LTD.

- NOTES:**
- 1. TIE-IN TO PLANT 13 SHOWN ON DRAWING 13-00-214.
 - 2. TYPICAL ARRANGEMENT FOR EACH UTILITY STATION
 - 3. PLANT 22 BATTERY LIMIT ISOLATION VALVE (LO) & SPECTACLE BLIND SHOWN ON DRG. 13-00-214 INSTALLED AS PART OF ETB PHASE.
 - 4. TYPICAL STEAM TRAP SUPPLY NO. OFF STEAM TRAPS TO SUIT PIPING DESIGN.
 - 5. FOR SYMBOLS, NOMENCLATURE, STANDARD DETAILS AND GENERAL NOTES REFER TO DWG. NO. 01-00-30-001 TO 011.
 - 6. PROJECT 5225 SCOPE IS WITHIN CLOUDED AREAS ONLY.
 - 7. VALVE TO BE LOCATED MIN 300MM ABOVE GRADE.
- PROJECT 5225 NOTES:**

0	24.06.2024	ISSUED FOR CONSTRUCTION (IFC)	PRA	VK/IV	YVR	WAM
B	14.06.2024	ISSUED FOR APPROVAL (IFA)	PRA	JM/IV	YVR	WAM
A	16.05.2024	ISSUED FOR COMPANY REVIEW (ICR)	PRA	JM/IV	YVR	WAM
REV	DATE	DESCRIPTION	DRAWN	CHKD	APPRD	APPRD (TARGET)

CONTRACTOR: **TARGET** ENGINEERING SUBCONTRACTOR: **BULFINGER**

PROJECT TITLE:
HABSHAN & BAB CONTROL SYSTEMS UPGRADE PACKAGE 1

CONTR. PROJ. No.: AET01074.00	CONT. DWG. No.: 3143673
ADNOC GAS AGREEMENT No.: 4700018747	ADNOC GAS PROJ. No.: 0405323

--	--	