


			ADNOC GAS HABSHAN & BAB CONTROL SYSTEMS UPGRADE (PACKAGE 1) PROJECT NO. 0405323						TARGET 				
			COMMENTS RESOLUTION SHEET										
Document Title:			PIPING & INSTRUMENTATION DIAGRAM FLARE, PURGE, AIR, WATER & NITROGEN SYSTEM UNIT 22 THAMMAMA 'C'			AGP Response Code			Prepared By:	VK			
Document No:			22-00-40001		Revision No:	B	1. Revise and Re-submit		3. Approved	X	Checked By:	DV	
AG Ref. No:			ADNOCGP-WTRAN-007987		Date:	20-Jun-2024	2. Approved with comments		4. For Information only		Approved By:	YVR	
SN	Reference		COMPANY Comments				CONSULTANT Response			COMPANY Resolution			
	Page No.	Clause No.											
1	1	-	No comment				-						

MASTER COPY

25-Jun-2024 idm260310

TEBODIN M.E. LTD.

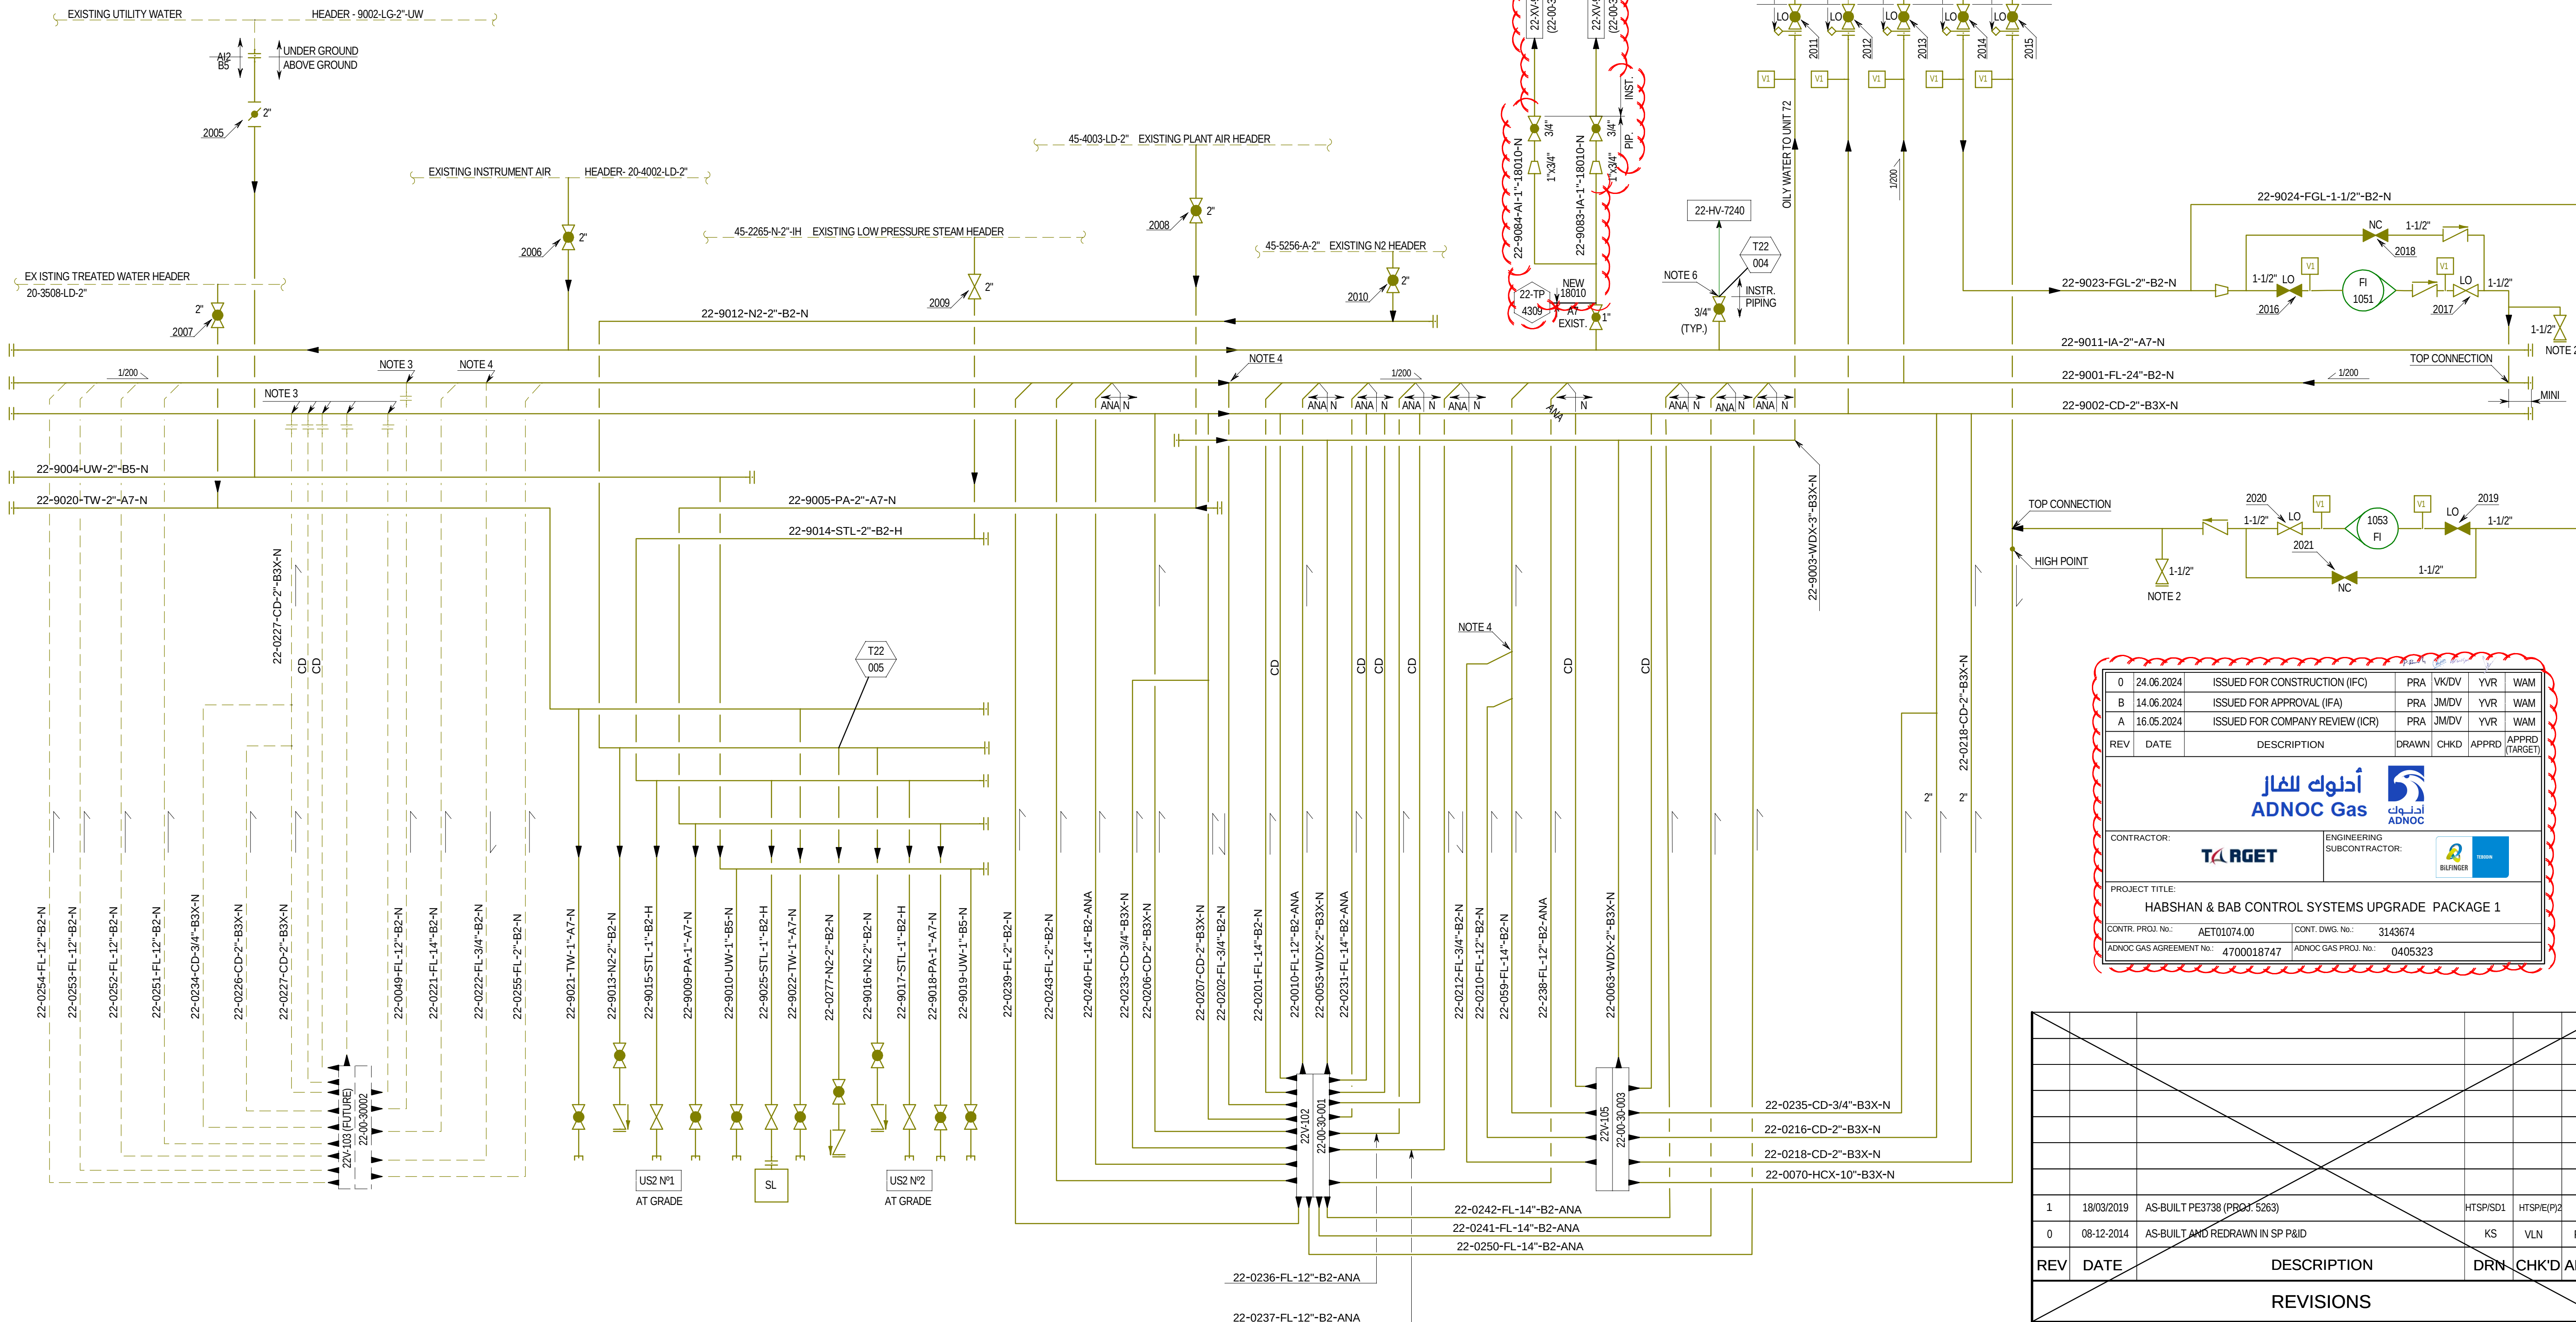


- NOTES:
- 1- DELETED
 - 2- FOR NITROGEN PURGING
 - 3- TIE IN POINT FUTURE EQUIPMENT 22V-103
 - 4- TOP CONNECTION. FOR DETAIL SEE DETAIL "A"
 - 5- DELETED
 - 6- EXISTING SPARE VALVE WILL BE USED FOR IA SUPPLY TO 22-HV-7240.

REFERENCE:-

1. 03-00-30001 TO 007 - LEGEND FOR HABSHAN-1

LEGENDS:-

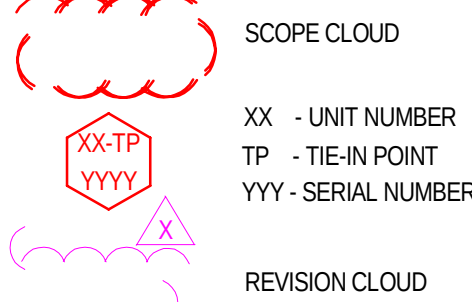

USE THIS DRAWING FOR INFORMATION GIVEN WITHIN CLOUDED AREA

THIS DRAWING IS DEVELOPED FROM ADNOC DRAWING NO. 22-00-40001 SHT 1/1, REV.1

0	24.06.2024	ISSUED FOR CONSTRUCTION (IFC)	PRA	VKIDV	YVR	WAM
B	14.06.2024	ISSUED FOR APPROVAL (IFA)	PRA	JMDIV	YVR	WAM
A	16.05.2024	ISSUED FOR COMPANY REVIEW (ICR)	PRA	JMDIV	YVR	WAM
REV	DATE	DESCRIPTION	DRAWN	CHKD	APPRD	APPRD (TARGET)
أدنوك للغاز ADNOC Gas ادئوك ADNOC						
CONTRACTOR:			ENGINEERING SUBCONTRACTOR:			
PROJECT TITLE:			HABSHAN & BAB CONTROL SYSTEMS UPGRADE PACKAGE 1			
CONTR. PROJ. No.:		AET01074.00	CONT. DWG. No.:		3143674	
ADNOC GAS AGREEMENT No.:		4700018747	ADNOC GAS PROJ. No.:		0405323	

REV	DATE	DESCRIPTION	DRN	CHK'D	APP'D
REVISIONS					
NOTICE:					
THIS DRAWING AND THE INFORMATION IT CONTAINS IS THE SOLE PROPERTY OF ABU DHABI GAS INDUSTRIES LTD. IT SHALL NOT BE REPRODUCED OR LENT WITHOUT THE AGREEMENT OF THE OWNER.					
DRAWN BY		INITIAL	ONSHORE GAS DEVELOPMENT PROJECT		
DATE					
CHK'D BY		INITIAL			
		SIGN			
DATE			PIPING & INSTRUMENTATION DIAGRAM FLARE, PURGE, AIR, WATER & NITROGEN SYSTEM UNIT 22 THAMMAMA 'C'		
CHK'D BY		INITIAL			
		SIGN			
DATE					
CHK'D BY		INITIAL	HABSHAN PROJECT NO.		JOB No.
		SIGN	2010 - 003		7600L
DATE			SCALE	PROJ. No.	UNIT No.
CHK'D BY		INITIAL	NTS	545	22
		SIGN	DRAWING No.		SHEET No.
DATE			22-00-40001		1/1
			REV.		1