

			ADNOC GAS HABSHAN & BAB CONTROL SYSTEMS UPGRADE (PACKAGE 1) PROJECT NO. 0405323						  			
			COMMENTS RESOLUTION SHEET									
Document Title:			PIPING AND INSTRUMENTATION DIAGRAM GAS TURBINE INSTRUMENT DIAGRAM FOR 13-C-102				AGP Response Code			Prepared By:	VK	
Document No:			5323P1-H1-013-00-50-001		Revision No:	B	1. Revise and Re-submit		3. Approved	Checked By:	DV	
AG Ref. No:			ADNOCGP-WTRAN-007250		Date:	6-Jun-2024	2. Approved with comments	✓	4. For Information only	Approved By:	YVR	
SN	Reference		COMPANY Comments				CONSULTANT Response			COMPANY Resolution		
	Page No.	Clause No.										
1	1	Process Comment	Hold shall be removed before submitting the next revision of the documents.				Noted and hold is removed from P&ID.					
2	1	-	-				Following changes are made in P&ID w.r.t. Rev.B submission as per instrumentation inputs: 1.Speed indicator SI-7515/7516 are shown in package-2 scope based on input. 2.Hold 2 is deleted from P&ID.					

NOTICE: THIS DRAWING AND THE INFORMATION IT CONTAINS IS THE SOLE PROPERTY OF ADNOC GAS PROCESSING. IT SHALL NOT BE REPRODUCED OR LENT WITHOUT THE AGREEMENT OF THE OWNER

MASTER COPY

12-Aug-2024 idm260310

TEBODIN M.E. LTD.


NOTES:-

- OPTIONAL THERMOCOUPLE HARNESS FOR INDIVIDUAL THERMOCOUPLE READOUT CONSISTS OF ELEVEN THERMOCOUPLES CONNECTED TO FOUR SEPARATE ENGINE MOUNTED CONNECTORS IN GROUPS OF THREE, TWO AND THREE FOR INTERFACE WITH CONTROL SYSTEM.
- SEE DRAWING 478-373-601 FOR DESCRIPTION OF SYMBOLS & LETTER DESIGNATION.
- SEE LM 2500 INSTALLATION DRAWING L31705 FOR DESCRIPTION AND LOCATION OF CONNECTIONS EI THRU E23.
- SEE DETACHED BILL OF MATERIAL 478-111-201.
- THE AREA CLASSIFICATION IS 13. ALL TO BE PROCEEDED BY 13. EG. 13-TE-5507.
- REFER TO BILL OF MATERIALS 478-111-203.
- VOTING IMPLEMENTED REF PCR 01-03 FOR DETAILS.
- EXISTING INSTRUMENT ARE REPLACED WITH NEW INSTRUMENT AS PER PROJECT (0405323) SCOPE.
- ALL INSTRUMENTS ALONG WITH PACKAGE DOCUMENTATION SHALL BE PROVIDED BY TURBINE OEM UNDER PACKAGE-2.
- INSTRUMENTS RELATED TO MMS SYSTEM ALONG WITH DOCUMENTATION SHALL BE PROVIDED BY MMS VENDOR.
- EXISTING LOCAL CONTROL PANEL IS REPLACED WITH NEW LOCAL CONTROL PANEL.
- THE TURBINE CONTROL SYSTEM (TCS) SHALL BE INTERFACED TO DCS THROUGH REDUNDANT MODBUS TCP/IP COMMUNICATION.
- THE EXISTING UNIT CONTROL PANEL (UCP) RELATED TO GE RX 3I AND WOODWARD IS REPLACED WITH NEW TURBINE CONTROL SYSTEM.

HOLDS:-

- DELETED
- DELETED

LEGENDS:-

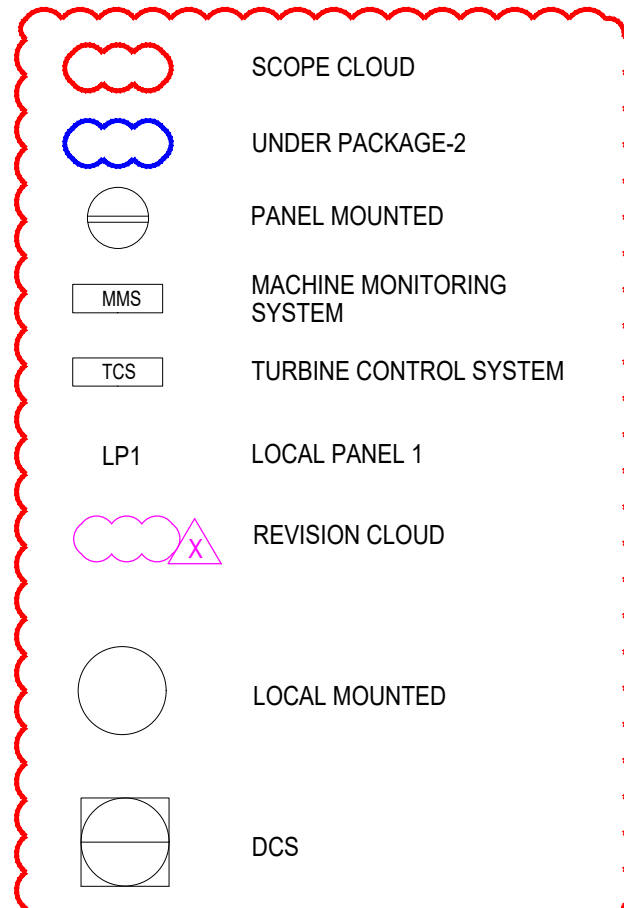

REFERENCE:-

- NM-5323P1-H1-013-15-21-001 - INSTRUMENT INDEX - UNIT 13
- 03-00-30001 TO 007 - LEGEND FOR HABSHAN-1
- NM-5323P1-H1-01-00-40-002 - ALARM AND TRIP SETTINGS LIST - HABSHAN 1

USE THIS DRAWING FOR INFORMATION GIVEN WITHIN CLOUDED AREA

THIS DRAWING IS DEVELOPED FROM ADNOC DRAWING NO. 478-111 SHT 1/2 REV 06 (PACKAGE / VENDOR DRAWING)

REV	DATE	DESCRIPTION	DRAWN	CHKD	APPRD	APPRD (TARGET)
0	09.08.2024	ISSUED FOR CONSTRUCTION (IFC)	PRA	VK/DV	YVR	WAM
B	27.05.2024	ISSUED FOR APPROVAL (IFA)	PRA	VK/DV	YVR	WAM
A	13.01.2024	ISSUED FOR COMPANY REVIEW (ICR)	PT	KG/TS	YVR	WAM

SCALE: NTS
DRAWN: PRA
CHKD: VK/DV
APPRD: YVR
APPRD (TARGET): WAM

CONTRACTOR: **ADNOC Gas**
ENGINEERING SUBCONTRACTOR: **ADNOC**


PROJECT TITLE: HABSHAN & BAB CONTROL SYSTEMS UPGRADE PACKAGE 1

DRAWING TITLE: PIPING AND INSTRUMENTATION DIAGRAM GAS TURBINE INSTRUMENT DIAGRAM FOR 13-C-102

UNIT: 13
CONTR. PROJ. No.: AET01074.00
PLANT: HABSHAN-1
CONT. DWG. No.: 3143221


ADNOC GAS PROJ. No.: 0405323
ADNOC GAS DWG. No.: 5323P1-H1-013-00-50-001
SHEET No.: 01/02
REV: 06
SHEET SIZE: A1

CONTRACT NO.	21712B	BY	DATE	INSTRUMENTATION
TYPE	INST	DRAWN	DLM	04/20/92
SCALE	NONE	CHECKED	TFD	04/21/92
DEPT.	63.811	REDRAW		
DRAFTING APPROVAL		DJL	04/21/92	
CONTRACT APPROVAL		JAB	04/21/92	
SYSTEM APPROVAL		TFD	04/21/92	
		LICD/SEE		

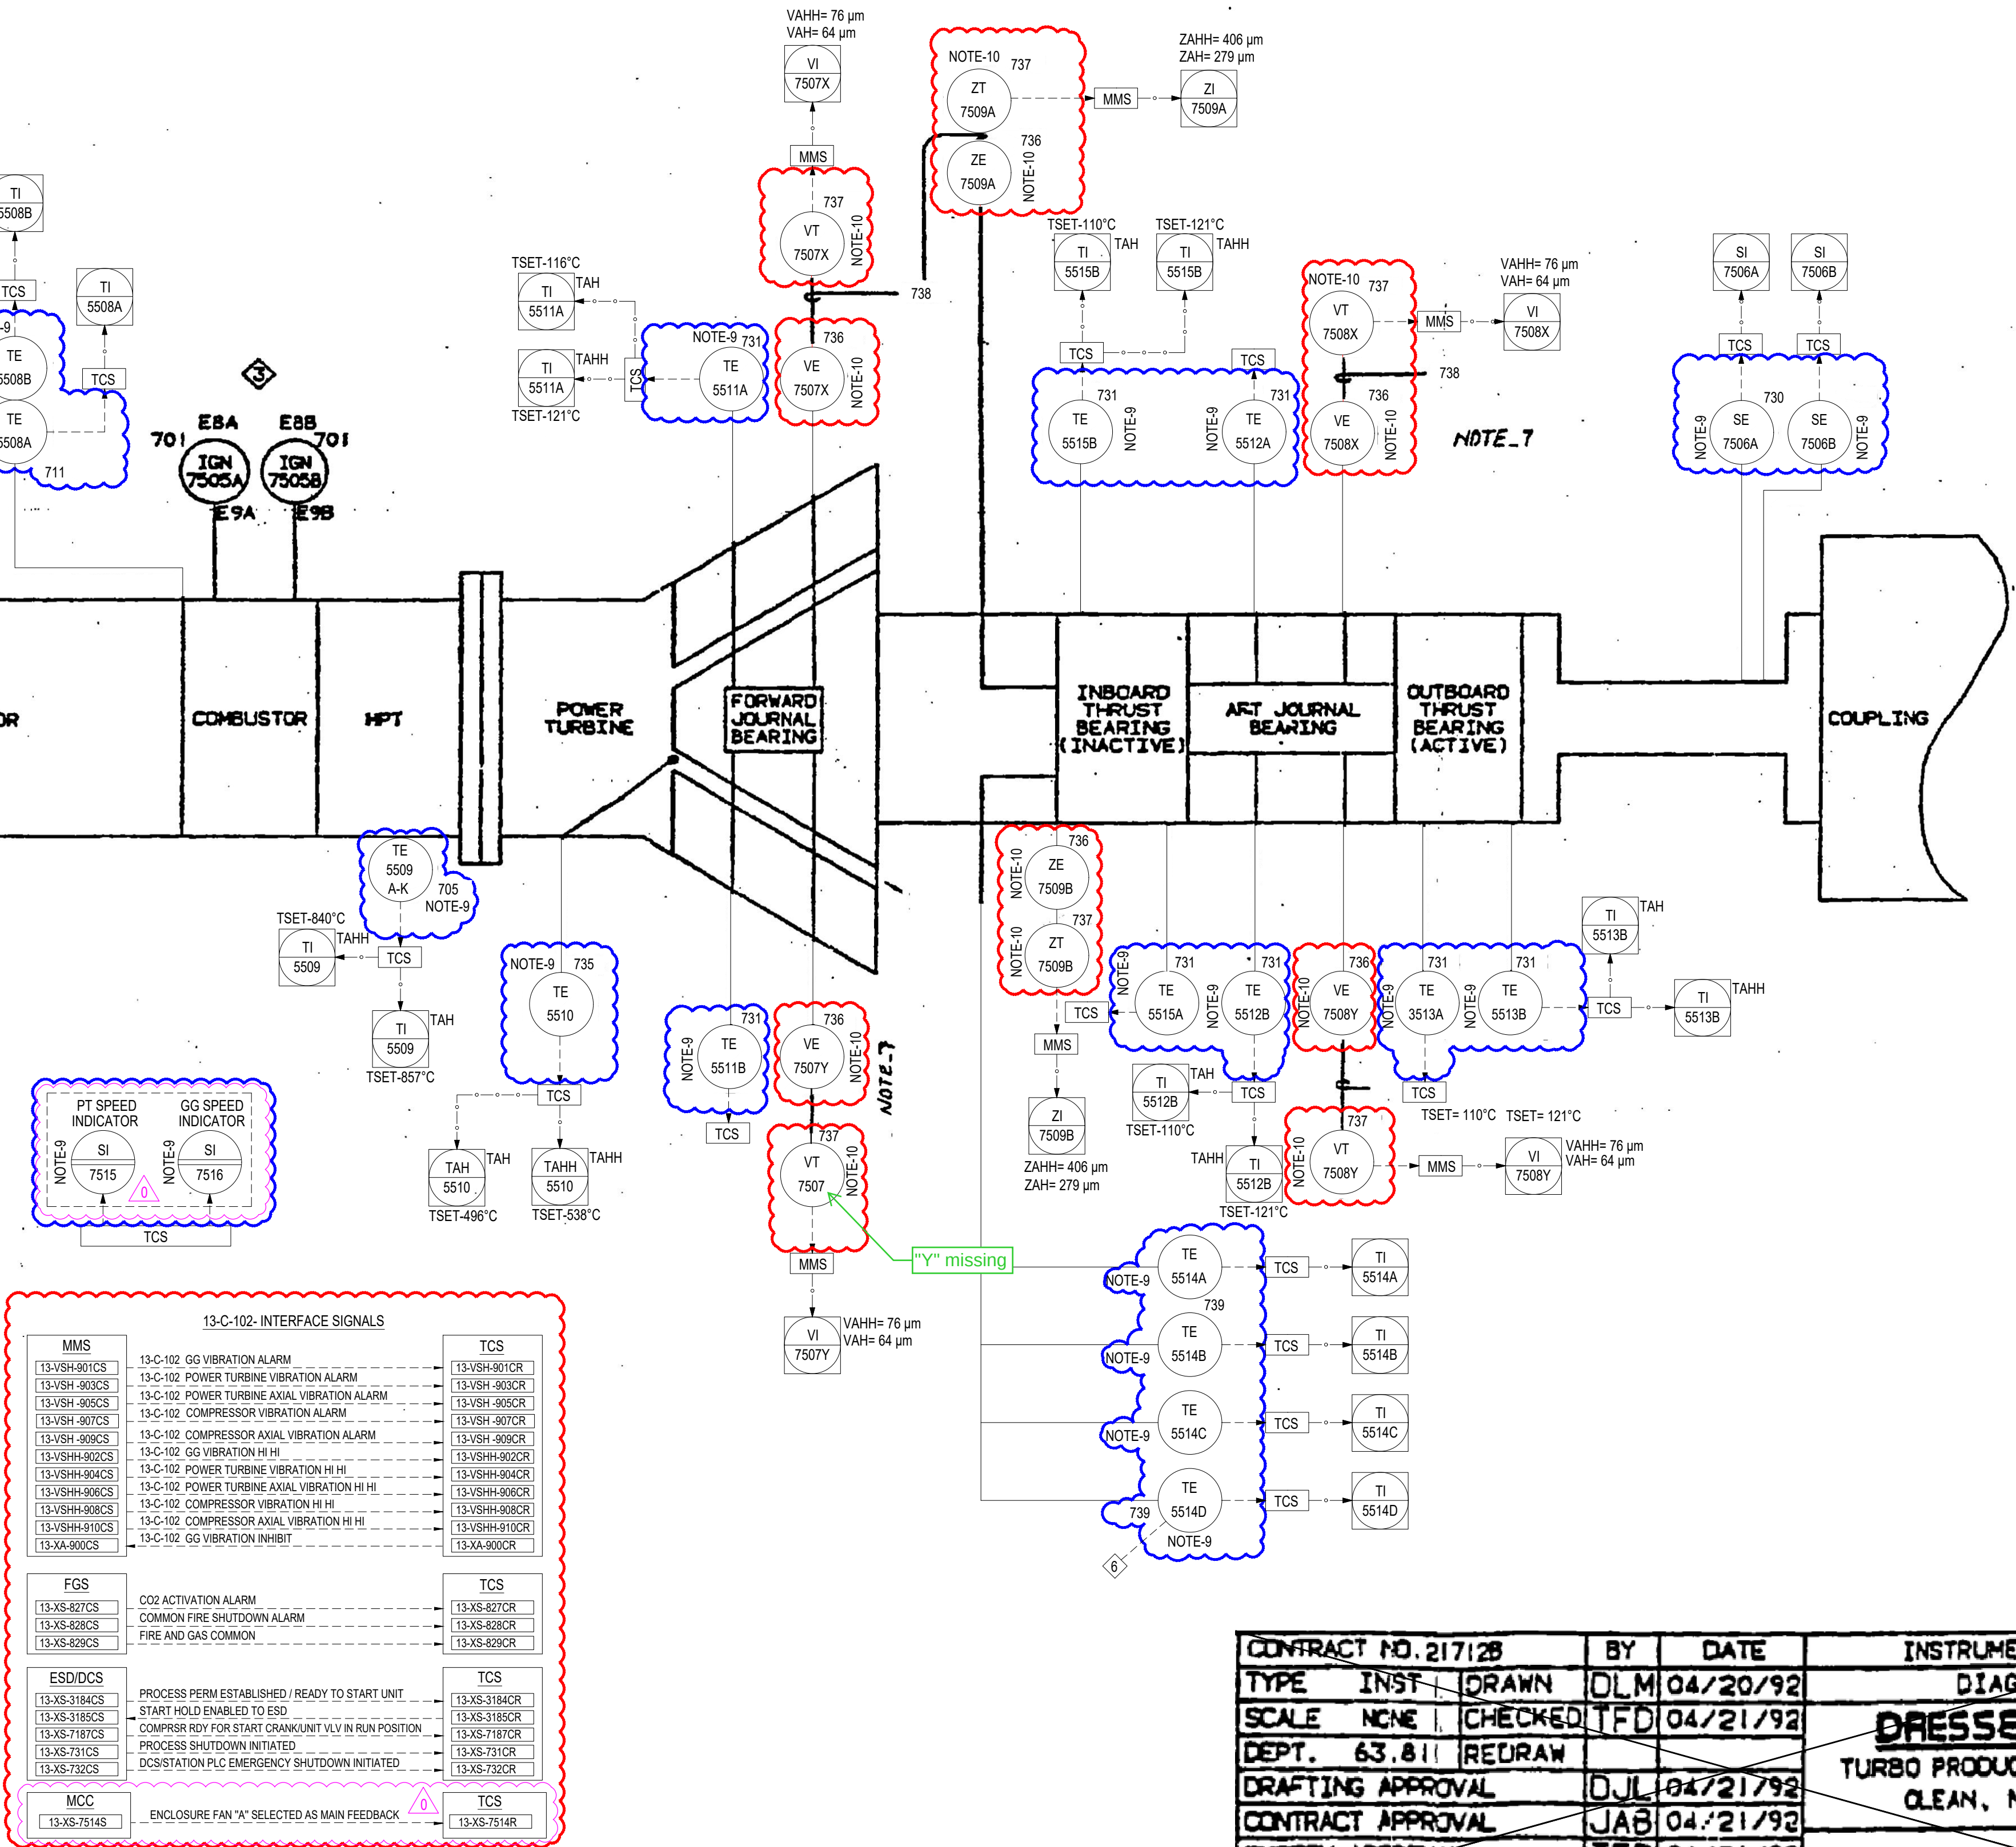

13-C-102- INTERFACE SIGNALS		
MMS	13-C-102	TCS
13-VSH-901CS	13-C-102 GG VIBRATION ALARM	13-VSH-901CR
13-VSH-902CS	13-C-102 POWER TURBINE VIBRATION ALARM	13-VSH-902CR
13-VSH-903CS	13-C-102 POWER TURBINE AXIAL VIBRATION ALARM	13-VSH-903CR
13-VSH-904CS	13-C-102 COMPRESSOR VIBRATION ALARM	13-VSH-904CR
13-VSH-905CS	13-C-102 COMPRESSOR AXIAL VIBRATION ALARM	13-VSH-905CR
13-VSH-906CS	13-C-102 GG VIBRATION HI HI	13-VSH-906CR
13-VSH-907CS	13-C-102 POWER TURBINE VIBRATION HI HI	13-VSH-907CR
13-VSH-908CS	13-C-102 POWER TURBINE AXIAL VIBRATION HI HI	13-VSH-908CR
13-VSH-909CS	13-C-102 COMPRESSOR VIBRATION HI HI	13-VSH-909CR
13-VSH-910CS	13-C-102 COMPRESSOR AXIAL VIBRATION HI HI	13-VSH-910CR
13-XA-900CS	13-C-102 GG VIBRATION INHIBIT	13-XA-900CR
FGS	13-C-102	TCS
13-XS-827CS	CO2 ACTIVATION ALARM	13-XS-827CR
13-XS-828CS	COMMON FIRE SHUTDOWN ALARM	13-XS-828CR
13-XS-829CS	FIRE AND GAS COMMON	13-XS-829CR
ESD/DCS	13-C-102	TCS
13-XS-3184CS	PROCESS PERM ESTABLISHED / READY TO START UNIT	13-XS-3184CR
13-XS-3185CS	START HOLD ENABLED TO ESD	13-XS-3185CR
13-XS-3186CS	COMPRESSOR FOR START CRANK/UNIT VLV IN RUN POSITION	13-XS-3186CR
13-XS-3187CS	PROCESS SHUTDOWN INITIATED	13-XS-3187CR
13-XS-3188CS	DCS/STATION PLC EMERGENCY SHUTDOWN INITIATED	13-XS-3188CR
13-XS-3189CS		13-XS-3189CR
MCC	13-C-102	TCS
13-XS-7514S	ENCLOSURE FAN "A" SELECTED AS MAIN FEEDBACK	13-XS-7514R

NOTICE: THIS DRAWING AND THE INFORMATION IT CONTAINS IS THE SOLE PROPERTY OF ADNOC GAS PROCESSING
IT SHALL NOT BE REPRODUCED OR LENT WITHOUT THE AGREEMENT OF THE OWNER

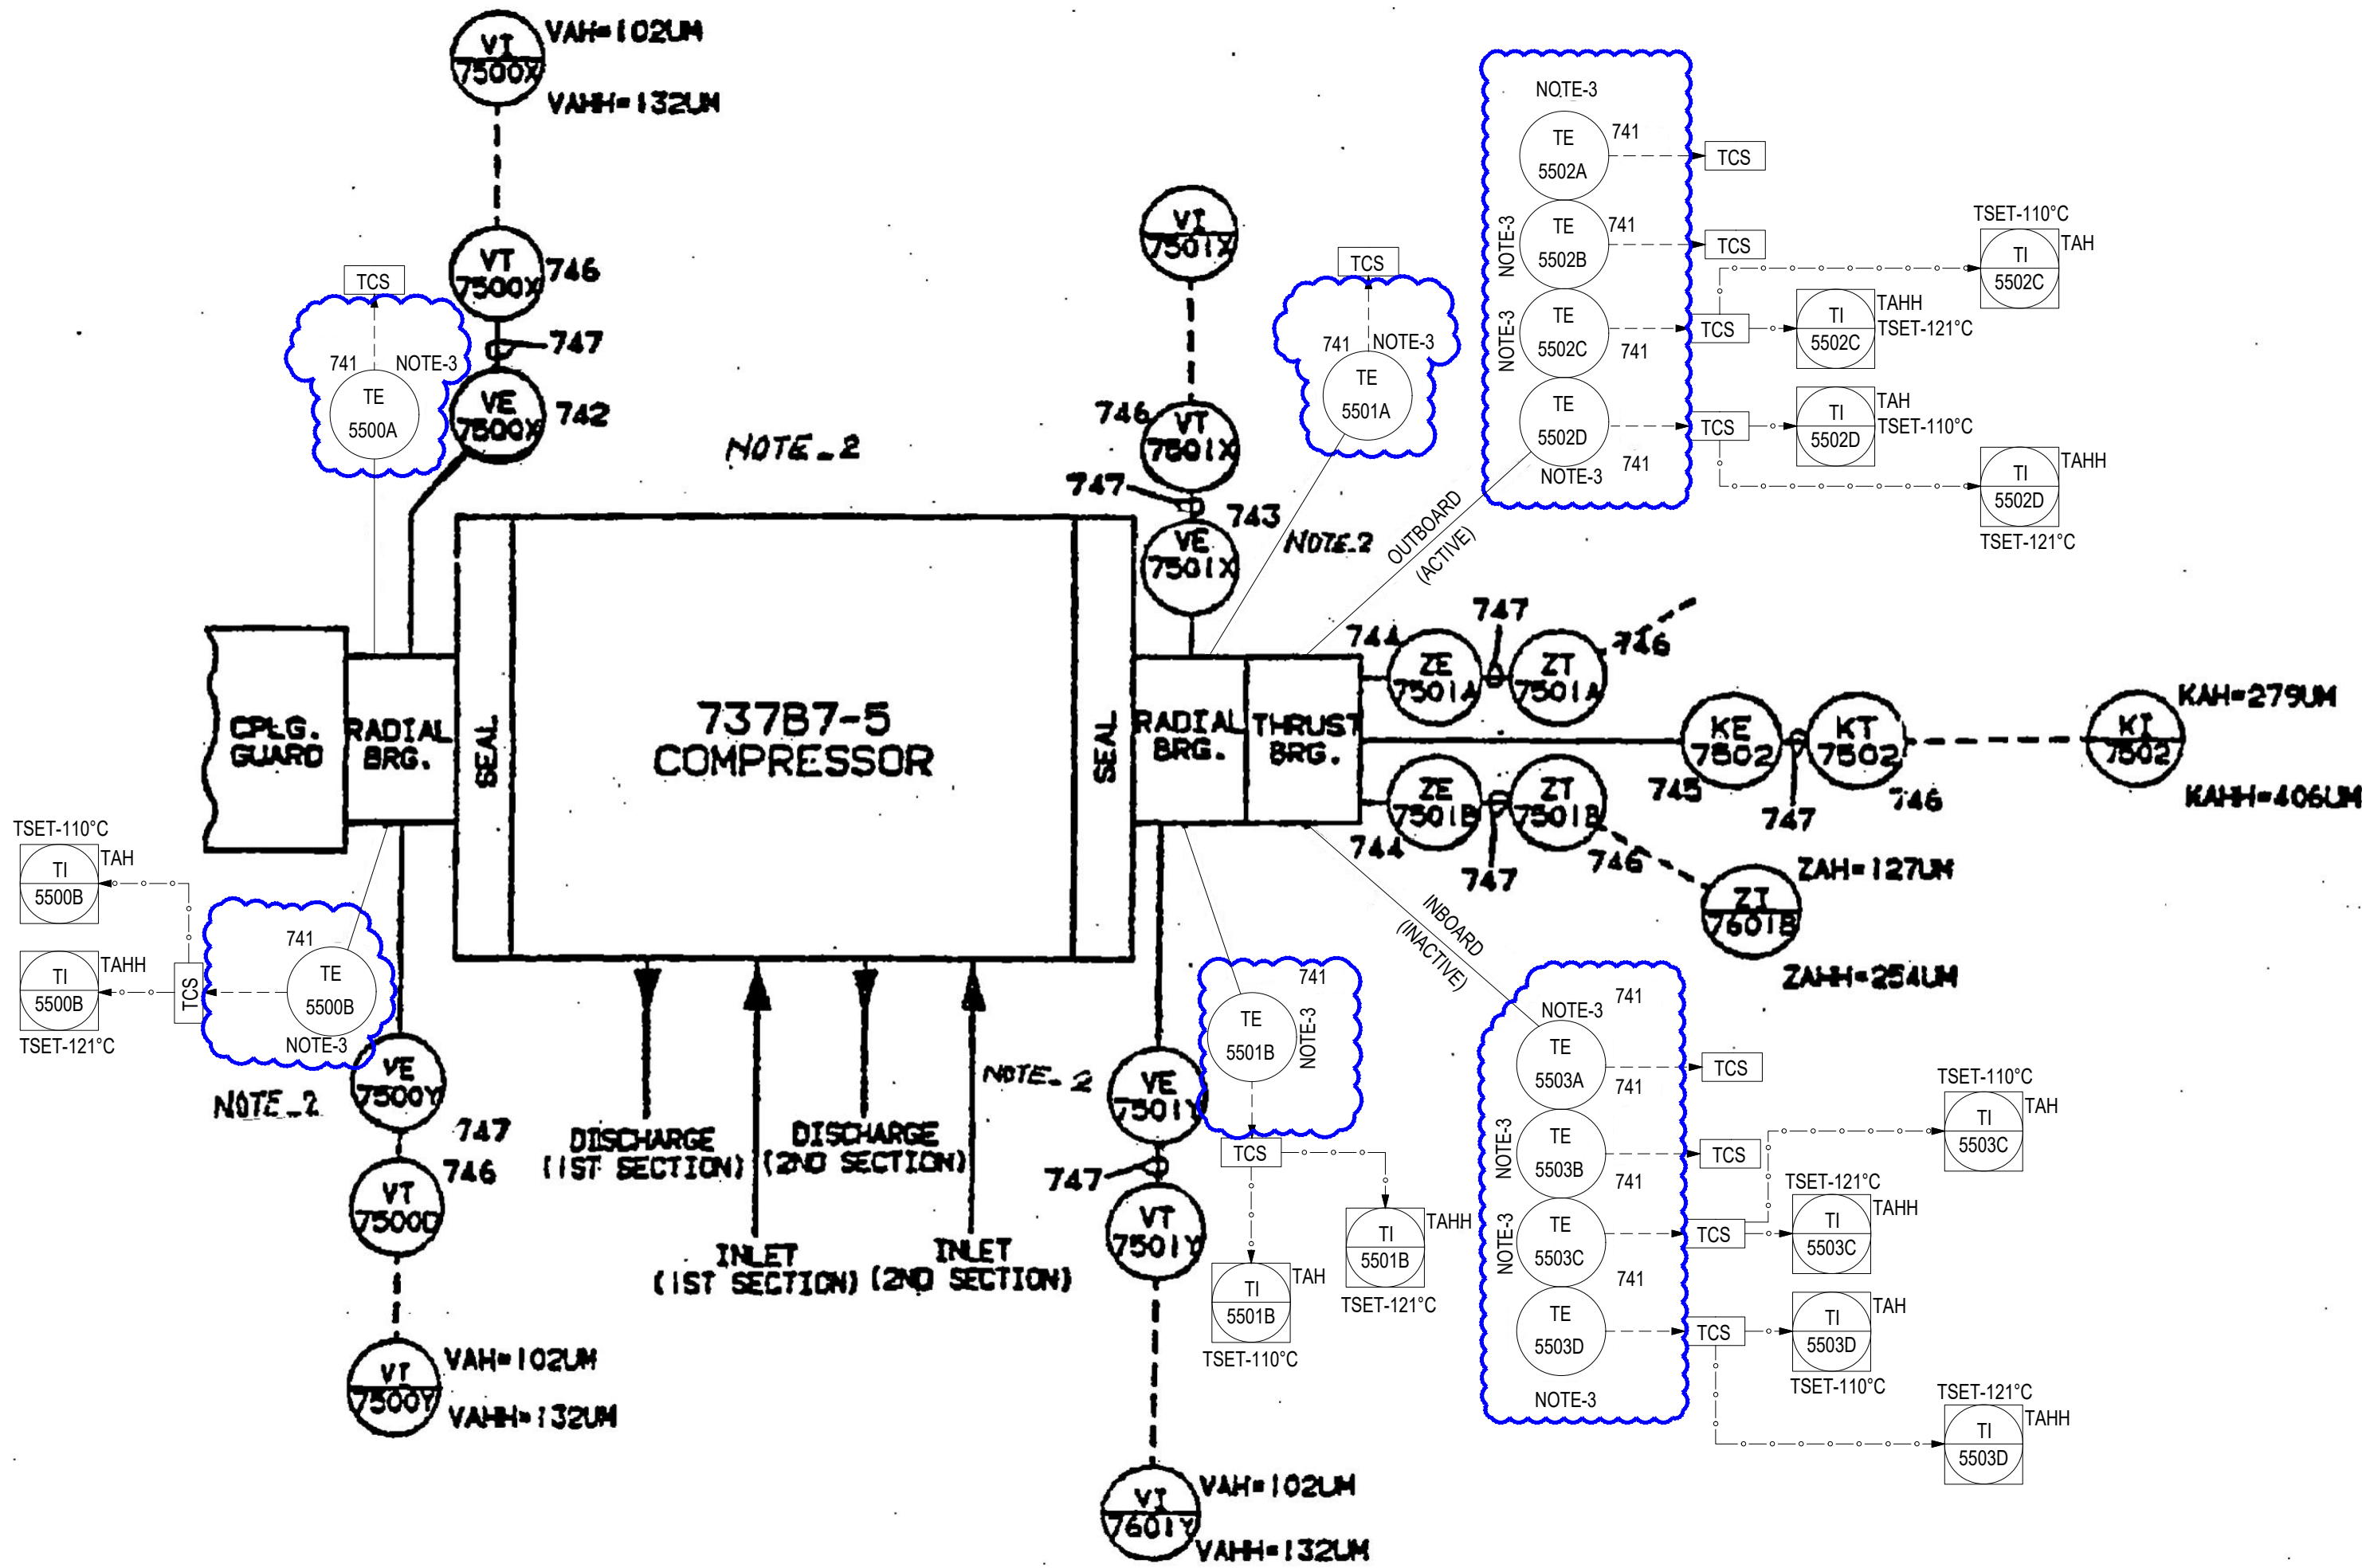

NOTES:-

- SEE DETACHED BILL OF MATERIAL 478-111-202.
- VOTING IMPLEMENTED REF PCR 01-03 FOR DETAILS.
- ALL INSTRUMENTS ALONG WITH PACKAGE DOCUMENTATION SHALL BE PROVIDED BY TURBINE OEM UNDER PACKAGE-2

LEGENDS:-

UNDER PACKAGE-2

USE THIS DRAWING FOR INFORMATION GIVEN WITHIN CLOUDED AREA

THIS DRAWING IS DEVELOPED FROM ADNOC DRAWING NO. 478-111 SHT 2/2 REV 06 (PACKAGE / VENDOR DRAWING)

REV	DATE	DESCRIPTION	DRAWN	CHKD	APPRD	APPRD (TARGET)
0	09.08.2024	ISSUED FOR CONSTRUCTION (IFC)	PRA	VK/DV	YVR	WAM
B	27.05.2024	ISSUED FOR APPROVAL (IFA)	PRA	VK/DV	YVR	WAM
A	13.01.2024	ISSUED FOR COMPANY REVIEW (ICR)	PT	KG/TS	YVR	WAM

CONTRACTOR:	ENGINEERING SUBCONTRACTOR:
ADNOC GAS	BILFINGER

PROJECT TITLE:	HABSHAN & BAB CONTROL SYSTEMS UPGRADE PACKAGE 1
DRAWING TITLE:	PIPING AND INSTRUMENTATION DIAGRAM GAS COMPRESSOR INSTRUMENT DIAGRAM FOR 13-C-102
UNIT:	13
PLANT:	HABSHAN-1
CONTR. PROJ. No.:	AET01074.00
CONT. DWG. No.:	3143221
ADNOC GAS AGREEMENT No.:	4700018747
ADNOC GAS PROJ. No.:	0405323
ADNOC GAS DWG. No.:	5323P1-H1-013-00-50-001
SHEET No.:	02/02
REV:	0

CONTRACT NO.	217128	BY	DATE	INSTRUMENTATION
TYPE	INST	DRAWN	DLM 04/20/92	DIAGRAM
SCALE	NONE	CHECKED	TFD 04/21/92	
DEPT.	63.81	REDRAW		
DRAFTING APPROVAL		DJL 04/21/92		
CONTRACT APPROVAL		JAB 04/21/92		
SYSTEM APPROVAL		TFD 04/21/92		
LICENSE				

DRESSER-RAND
TURBO PRODUCTS DIV
CLEAN, N Y USA

478-111 SHT. REV. 2 OF 2 06

CAD NO.: 5323P1-H1-013-00-50-001-02.DWG