

			ADNOC GAS HABSHAN & BAB CONTROL SYSTEMS UPGRADE (PACKAGE 1) PROJECT NO. 0405323						  			
			COMMENTS RESOLUTION SHEET									
Document Title:			PIPING AND INSTRUMENTATION DIAGRAM GAS COMPRESSOR POWER TURBINE INSTRUMENT FOR 13-C-101A/B			AGP Response Code			Prepared By:	VK		
Document No:			5323P1-H1-013-00-50-003		Revision No:	B	1. Revise and Re-submit		3. Approved	Checked By:	DV	
AG Ref. No:			ADNOCGP-WTRAN-007250		Date:	6-Jun-2024	2. Approved with comments	✓	4. For Information only	Approved By:	YVR	
SN	Reference		COMPANY Comments				CONSULTANT Response			COMPANY Resolution		
	Page No.	Clause No.										
1	1	Process Comment	Hold shall be removed before submitting the next revision of the documents.				Noted and hold is removed from P&ID.					
2	-	-	-				Following changes are made in P&ID w.r.t. Rev.B submission as per instrumentation inputs: 1.Speed indicator SI-7615/7616 are shown in package-2 scope 2.Hold 2 is deleted from P&ID. 3. Note 14 added. 4. Table to mention instruments in project scope for 13-C-101A and 13-C-101B is added. Refer detail "B".					

NOTICE: THIS DRAWING AND THE INFORMATION IT CONTAINS IS THE SOLE PROPERTY OF ADNOC GAS PROCESSING
IT SHALL NOT BE REPRODUCED OR LENT WITHOUT THE AGREEMENT OF THE OWNER

MASTER COPY

12-Aug-2024 idm260310

TEBODIN M.E. LTD.


NOTES:-

- OPTIONAL THERMOCOUPLE HARNESS FOR INDIVIDUAL THERMOCOUPLE READOUT CONSISTS OF ELEVEN THERMOCOUPLES CONNECTED TO FOUR SEPARATE ENGINE MOUNTED CONNECTORS IN GROUPS OF THREE. THREE, TWO AND THREE FOR INTERFACE WITH CONTROL SYSTEM.
- SEE DRAWING 478-373-601 FOR DESCRIPTION OF SYMBOLS & LETTER DESIGNATION.
- SEE LM 2500 INSTALLATION DRAWING L31705 FOR DESCRIPTION AND LOCATION OF CONNECTIONS EI THRU E23.
- SEE DETACHED BILL OF MATERIAL 478-111-201.
- THE AREA CLASSIFICATION IS 13 ALLTAG NO. 'S' ARE TO BE PROCEEDED BY 13. 'D' UNIT TAG NUMBERS ARE 100 HIGHER THAN 'C' UNIT EX, 13-TE 5610 FOR 'C' UNIT 13-TE 5710 FOR 'D' UNIT
- REFER TO BILL OF MATERIALS 478-111-203.
- EXISTING INSTRUMENT ARE REPLACED WITH NEW INSTRUMENT AS PER PROJECT (0405323) SCOPE
- ALL INSTRUMENTS ALONG WITH PACKAGE DOCUMENTATION SHALL BE PROVIDED BY TURBINE OEM UNDER PACKAGE-2
- INSTRUMENTS RELATED TO MMS SYSTEM ALONG WITH DOCUMENTATION SHALL BE PROVIDED BY MMS VENDOR.
- INSTRUMENTS APPLICABLE FOR GAS COMPRESSOR POWER TURBINE FOR 13-C-101A AS PER PROJECT (0405323) SCOPE SHALL BE APPLICABLE FOR 13-C-101B ALSO.
- EXISTING LOCAL CONTROL PANEL IS REPLACED WITH NEW LOCAL CONTROL PANEL.
- THE TURBINE CONTROL SYSTEM (TCS) SHALL BE INTERFACED TO DCS THROUGH REDUNDANT MODBUS TCP/IP COMMUNICATION.
- THE EXISTING UNIT CONTROL PANEL (UCP) RELATED TO GE RX 3I AND WOODWARD IS REPLACED WITH NEW TURBINE CONTROL SYSTEM.
- REFER DETAIL "B" FOR LIST OF INSTRUMENTS/VALVES, WHICH ARE REPLACED OR ADDED AS PER PROJECT (0405323) SCOPE.

HOLDS:-

- DELETED
- DELETED

LEGENDS:-

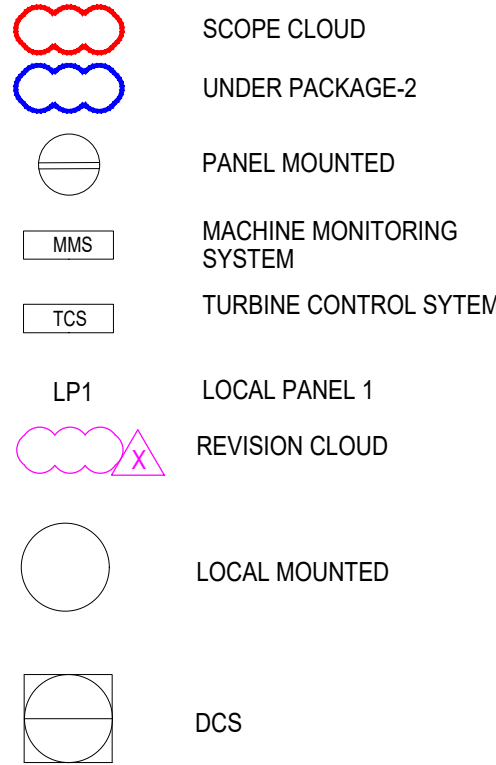

REFERENCE:-

- NM-5323P1-H1-013-15-21-001 - INSTRUMENT INDEX - UNIT 13
- 03-00-30001 TO 007 - LEGEND FOR HABSHAN-1
- NM-5323P1-H1-01-00-40-002 - ALARM AND TRIP SETTINGS LIST - HABSHAN 1


USE THIS DRAWING FOR INFORMATION GIVEN WITHIN CLOUDED AREA

THIS DRAWING IS DEVELOPED FROM ADNOC DRAWING NO. 478-129 SHT 1/2 REV 06 (PACKAGE / VENDOR DRAWING)


REV	DATE	DESCRIPTION	DRAWN	CHKD	APPRD	APPRD (TARGET)
0	09.08.2024	ISSUED FOR CONSTRUCTION (IFC)	PRA	VK/DV	YVR	WAM
B	27.05.2024	ISSUED FOR APPROVAL (IFA)	PRA	VK/DV	YVR	WAM
A	13.01.2024	ISSUED FOR COMPANY REVIEW (ICR)	PT	KG/TS	YVR	WAM

SCALE: NTS
DRAWN: PRA
CHKD: VK/DV
APPRD: YVR
APPRD (TARGET): WAM

CONTRACTOR: ADNOC Gas		ENGINEERING SUBCONTRACTOR: TARGET	
PROJECT TITLE: HABSHAN & BAB CONTROL SYSTEMS UPGRADE PROJECT NO.323-DEFINE STAGE			
DRAWING TITLE: PIPING AND INSTRUMENTATION DIAGRAM GAS COMPRESSOR POWER TURBINE INSTRUMENT FOR 13-C-101A/B			
UNIT: 13	PLANT: HABSHAN-1	CONTR. PROJ. No.: AET01074.00	CONT. DWG. No.: 3143223
ADNOC GAS AGREEMENT No.: 4700018747		ADNOC GAS PROJ. No.: 0405323	
ADNOC GAS DWG. No.: 5323P1-H1-013-00-50-003		SHEET No.: 01/02	
REV: 0		SHEET SIZE: A1	

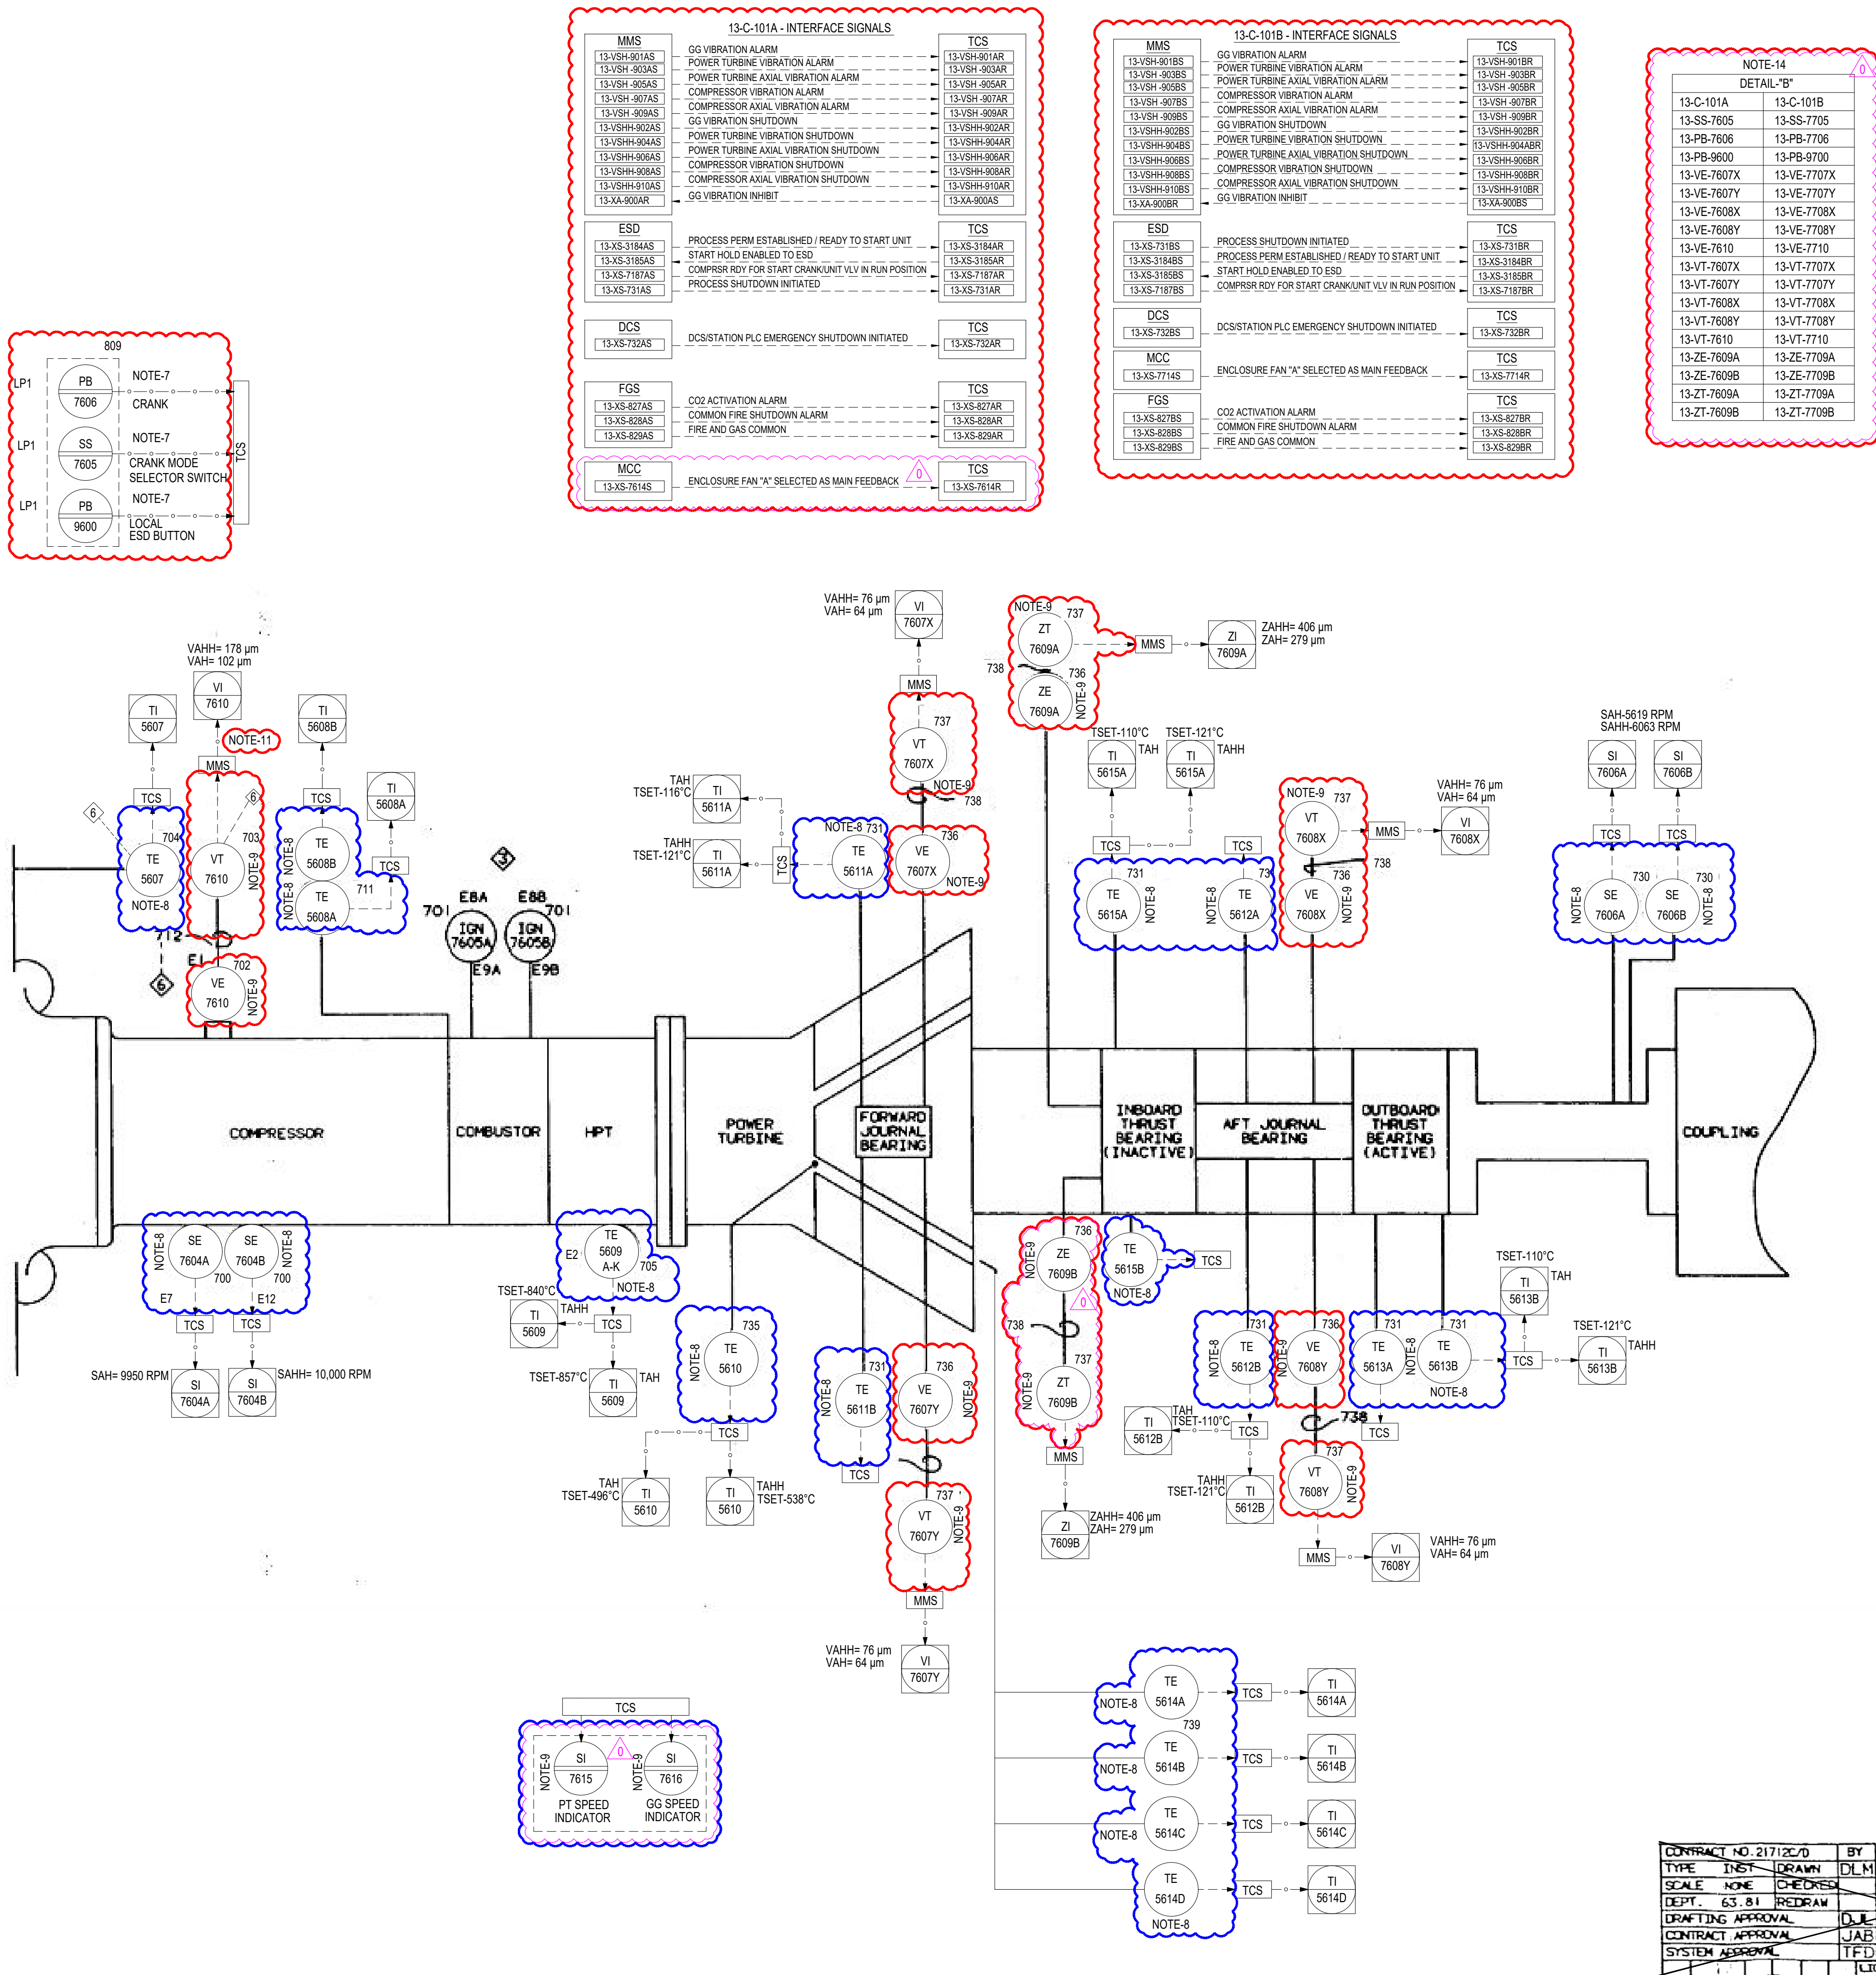

CONTRACT NO. 21712C/D	BY	DATE	INSTRUMENTATION
TYPE	INST	DRAWN	DLM
SCALE	NONE	CHECKED	04/20/92
DEPT.	63.81	REDRAWN	
DRAFTING APPROVAL	04/21/92		
CONTRACT APPROVAL	04/21/92		
SYSTEM APPROVAL	04/21/92		
478-129		SHT	REV
		1	06

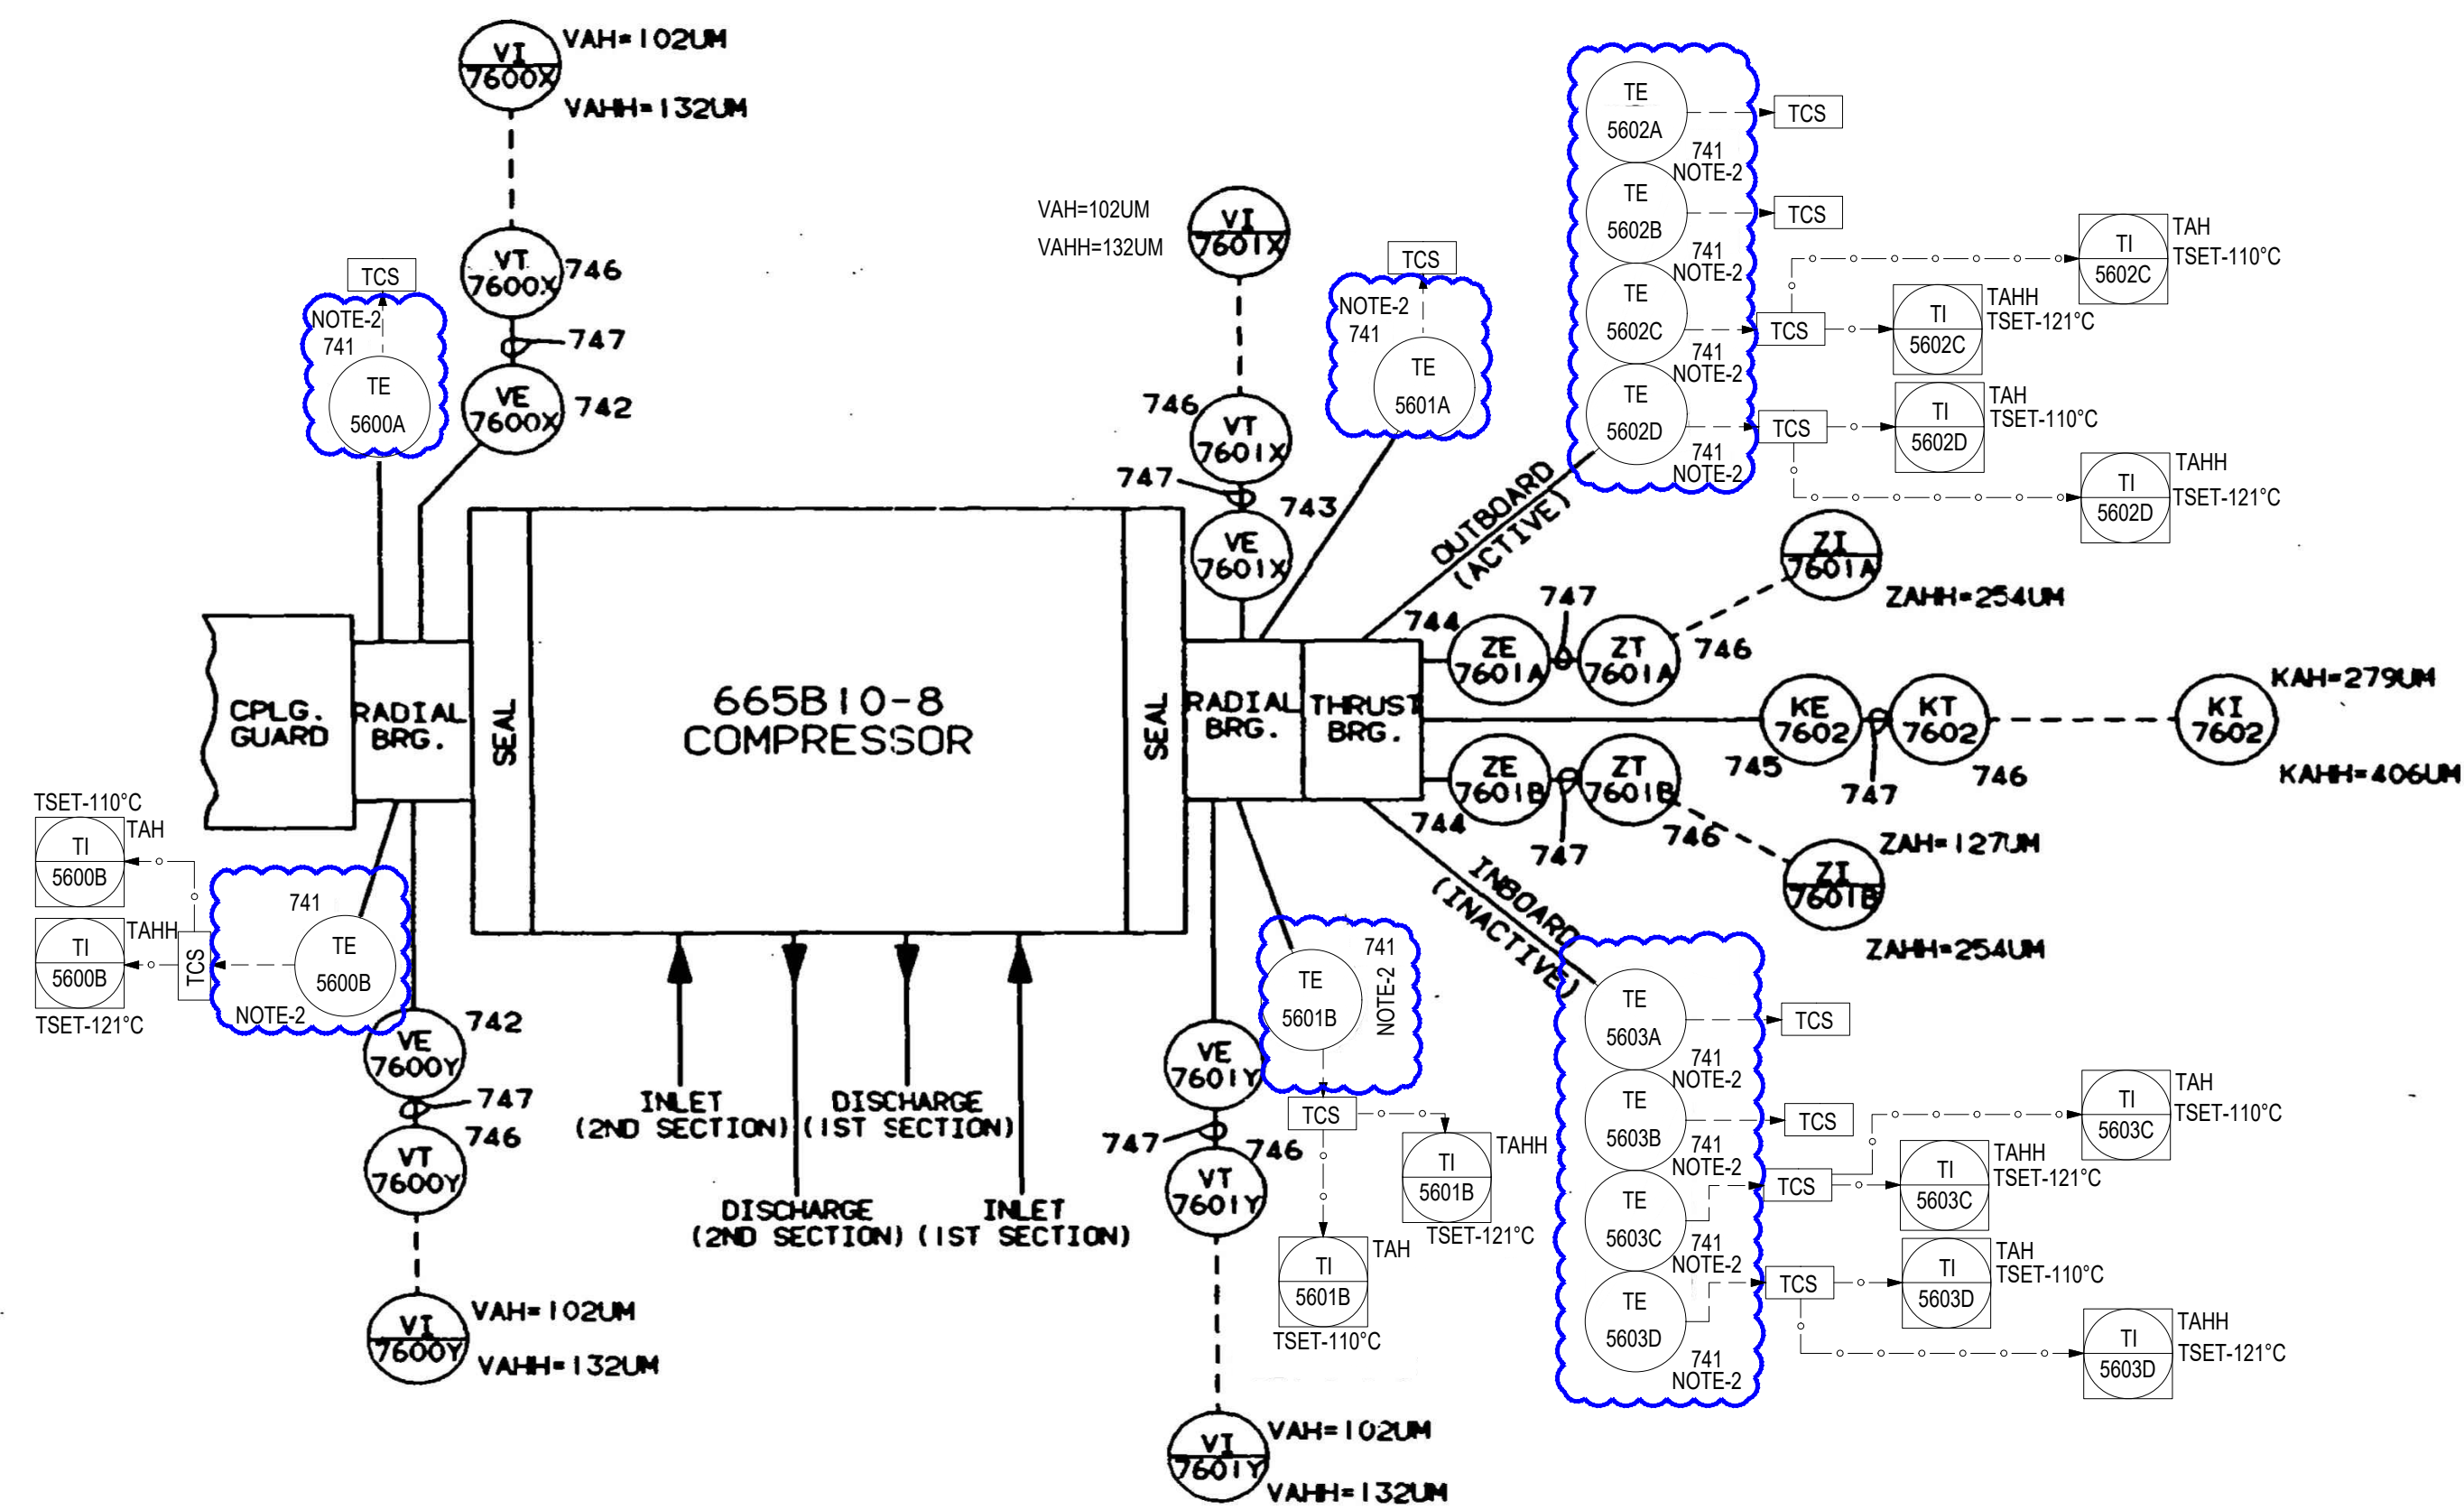


NOTES:

1. SEE DETACHED BILL OF MATERIAL 478-129-202.
2. ALL INSTRUMENTS ALONG WITH PACKAGE DOCUMENTATION SHALL BE PROVIDED BY TURBINE OEM UNDER PACKAGE-2.

LEGENDS:-



UNDER PACKAGE-2

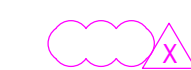

REVISION CLOUD

USE THIS DRAWING FOR INFORMATION GIVEN WITHIN
CLOUDED AREA

THIS DRAWING IS DEVELOPED FROM ADNOC DRAWING NO.
478-129 SHT 2/2 REV 06 (PACKAGE / VENDOR DRAWING)

[illegible]

CONTRACTOR: 



PROJECT TITLE:	HABSHAN & BAB CONTROL SYSTEMS UPGRADE PROJECT NO.323-DEFINE STAGE
----------------	--

DRAWING TITLE:	PIPING AND INSTRUMENTATION DIAGRAM
	GAS COMPRESSOR POWER TURBINE
	INSTRUMENT FOR 13-C-101A/B

UNIT: 13		PLANT: HABSHAN-1	
CONTR. PROJ. No.: AET01074.00		CONT. DWG. No.: 3143223	
ADNOC GAS AGREEMENT No.: 4700018747			
ADNOC GAS PROJ. No.: 0405323	ADNOC GAS DWG. No.: 5323P1-H1-013-00-50-003	SHEET No.: 02/02	REV: 0

CONTRACT NO. 2:712C/O		BY	DATE	INSTRUMENTATION	
TYPE	JNST	DRAWN	DLM	04/20/92	DIAGRAM
SCALE	NONE	CHECKED			DRESSER-RAND
DEPT.	63.81	REDRAW			TURBO PRODUCTS DIV
DRAFTING APPROVAL		D.L.	04/21/92	CLEAN, N.Y. USA	
CONTRACT APPROVAL		JAB	04/21/92	478-129	
SYSTEM APPROVAL		TFD	04/21/92		
		LUCAS		SHT.	REV.
				2 of 2	06

CAD NO.: 5323P1-H1-013-00-50-003-02.DWG

NOTICE: THIS DRAWING AND THE INFORMATION IT CONTAINS IS THE SOLE PROPERTY OF ADNOC GAS PROCESSING. IT SHALL NOT BE REPRODUCED OR LENT WITHOUT THE AGREEMENT OF THE OWNER