

			ADNOC GAS HABSHAN & BAB CONTROL SYSTEMS UPGRADE (PACKAGE 1) PROJECT NO. 0405323						  				
			COMMENTS RESOLUTION SHEET										
Document Title:			PIPING AND INSTRUMENTATION DIAGRAM GAS GENERATOR LUBE OIL SYSTEM FOR 13-C-101A/B/102				AGP Response Code			Prepared By:	VK		
Document No:			5323P1-H1-013-00-50-014		Revision No:	B	1. Revise and Re-submit	☐	3. Approved	☒	Checked By:	DV	
AG Ref. No:			ADNOCGP-WTRAN-007148		Date:	3-Jun-2024	2. Approved with comments	☐	4. For Information only	☐	Approved By:	YVR	
SN	Reference		COMPANY Comments				CONSULTANT Response			COMPANY Resolution			
	Page No.	Clause No.											
1	-	-	No Comments.				-						
2	1	-	-				Following changes are made in P&ID w.r.t. Rev.B submission as per piping/instrumentation inputs. 1. Root valves for all PT/PDT and LT are shown in project scope cloud based on instrument input. 2. New thermowell are added for TE-5546 and 5547 considering new tie-in location based on Piping Input. 3. Note 17 is updfated. 4. Tie-in Point 13-TP-A & C location is updated as per piping input. 5.New Tie-in point 13-TP-D is added as per piping Input. 6. Note 21 added. 7. Table to mention instruments in project scope for13-C-102, 13-C-101A and 13-C-101B is added. Refer detail "B".						

NOTICE: THIS DRAWING AND THE INFORMATION IT CONTAINS IS THE SOLE PROPERTY OF ADNOC GAS PROCESSING. IT SHALL NOT BE REPRODUCED OR LENT WITHOUT THE AGREEMENT OF THE OWNER

MASTER COPY

15-Aug-2024 IDM26031C

TEBODIN M.E. LTD.

NOTES:-

- FOR COMPONENT DESCRIPTION SEE BILLS OF MATERIAL #317-210-201, 317-210-202, 317-210-203 AND 317-210-204.
- FOR CUSTOMER CONNECTION LETTER DESCRIPTION SEE DRAWING #478-139-601.
- FOR PIPING LINE CODE EXPLANATION SEE DRAWING #003-152-001.
- FOR COMPONENT SYMBOLS AND LETTER DESIGNATIONS SEE DRAWING #478-373-601.
- FLUSHING STRAINERS ARE TO BE REMOVED ONLY AFTER FLUSHING IS COMPLETE.
- REFERENCE DRAWINGS
GG LUBE OIL CONSOLE DIAGRAM # 317-209
OIL CONSOLE WIRING DIAGRAM # 478-125
UTILITY LIST # 478-554
INSTRUMENT INDEX, CT-21712 B # 003-175-151
CT-21712 C/D # 003-175-152
LOCAL PANEL GENERAL ARRANGEMENT - LP1 # 478-450-601
LOCAL PANEL WIRING DIAGRAM - LP1 # 478-131
TURBINE SKID PS & GP GENERAL ARRANGEMENT - LP2 # 478-127
TURBINE SKID PS & GP WIRING DIAGRAM - LP2 # 478-132
OUTLINE AND FOUNDATION CT-21712 B # 478-144
CT-21712 C/D # 478-241
- PIPING HIGH POINT VENTS AND LOW POINT DRAINS TO BE PROVIDED.
- PIPING PER D-R SPEC. 003-230-001 AND DEVADD 003-230-017.
- PRIOR TO OPERATION OF UNIT RESERVOIR, REFERENCE PRESSURE LINE TO LEVEL TRANSMITTER MUST BE FILLED WITH MIL L 23699 OIL. LINE IS FULL WHEN OIL RUNS OUT OF TELL-TALE DRAIN VALVE. THE FILL DRAIN AND BLEED VALVES MUST BE CLOSED BEFORE STARTING ENGINE.
- FOR ADNOC MP BOOSTER PACKAGE CT 21712B INSTRUMENT TAG NUMBERS WILL BE IN THE FIVE (5) HUNDRED SERIES PREFACED BY AREA LOCATION NUMBER (13), 13-TE-7500
FOR ADNOC FEED GAS PACKAGE "A"-CT21712C, INSTRUMENT TAG NUMBERS WILL BE IN THE SIX (6) HUNDRED SERIES PREFACED BY AREA LOCATION NUMBER (13), 13-TE-7600
FOR ADNOC FEED GAS PACKAGE "B"-CT21712D, INSTRUMENT TAG NUMBERS WILL BE IN THE SEVEN (7) HUNDRED SERIES PREFACED BY AREA LOCATION NUMBER (13), 13-TE-7700
- EXISTING INSTRUMENT/VALVES ARE REPLACED WITH NEW INSTRUMENT/VALVES AS PER PROJECT (0405323) SCOPE.
- FOR UNIT 13-C-102 & 13-C-101A CORRESPONDING EXISTING INSTRUMENT/VALVES ARE REPLACED WITH NEW INSTRUMENT / VALVES AS PER PROJECT (0405323) SCOPE.
- FOR UNIT 13-C-102 CORRESPONDING EXISTING INSTRUMENT/VALVES ARE REPLACED WITH NEW INSTRUMENT/VALVES AS PER PROJECT (0405323) SCOPE.
- FOR UNIT 13-C-102 & 13-C-101A/B, NEW TEMPERATURE TRANSMITTER NEEDS TO BE INSTALLED FOR THE CORRESPONDING TEMPERATURE ELEMENT AS PER PROJECT (0405323) SCOPE.
- ALL PIPING INSTRUMENT INTERFACE CONNECTION WILL BE AS PER HOOK-UP DIAGRAM (5323P1-H1-01-15-38-001 & 5323P1-H1-01-15-38-002).
- FOR UNIT 13-C-101B, EXISTING INSTRUMENT 13-TE-5747 IS RETAINED.
- NEW THERMOWELL TO BE PROVIDED FOR FOR UNIT 13-C-102 & 13-C-101A/B.
- FOR UNIT 13-C-101A/B EXISTING INSTRUMENT 13-TE-5646, 13-TE-5746 IS RETAINED.
- THE TURBINE CONTROL SYSTEM (TCS) SHALL BE INTERFACED TO DCS THROUGH REDUNDANT MODBUS TCP/IP COMMUNICATION.
- THE EXISTING UNIT CONTROL PANEL (UCP) RELATED TO GE RX 31 AND WOODWARD IS REPLACED WITH NEW TURBINE CONTROL SYSTEM.
- REFER DETAIL "B" FOR LIST OF INSTRUMENTS/VALVES, WHICH ARE REPLACED OR ADDED AS PER PROJECT (0405323) SCOPE.

LEGENDS:-

SCOPE CLOUD	REVISION CLOUD
TCS	LOCAL MOUNTED
LP2	DCS
XX-TP	XX - UNIT NUMBER
YYY	TP - TIE-IN POINT
	YYY - SERIAL NUMBER
PANEL MOUNTED	VALVE - INST. OR GLOBE - NOR. OPEN
	VALVE - INST. OR GLOBE - NOR. CLOSED

REFERENCE:-

- NM-5323P1-H1-013-15-21-001 - INSTRUMENT INDEX - UNIT 13
- 03-00-30001 TO 007 - LEGEND FOR HABSHAN-1
- NM-5323P1-H1-01-00-40-002 - ALARM AND TRIP SETTINGS LIST - HABSHAN 1

USE THIS DRAWING FOR INFORMATION GIVEN WITHIN CLOUDED AREA


THIS DRAWING IS DEVELOPED FROM ADNOC DRAWING NO. 317-210 SHT 1/1 REV 03 (PACKAGE / VENDOR DRAWING)

REV	DATE	DESCRIPTION	DRAWN	CHKD	APPRD	APPRD (TARGET)
0	14.08.2024	ISSUED FOR CONSTRUCTION (IFC)	PRA	VK/DV	YVR	WAM
B	27.05.2024	ISSUED FOR APPROVAL	PRA	KG/DV	YVR	WAM
A	13.01.2024	ISSUED FOR COMPANY REVIEW (ICR)	PT	KG/TS	YVR	WAM

SCALE: NTS
DRAWN: PRA
CHKD: VK/DV
APPRD: YSV
APPRD (TARGET): WAM

CONTRACTOR:	ENGINEERING SUBCONTRACTOR:
TARGET	BILFINGER

PROJECT TITLE:		HABSHAN & BAB CONTROL SYSTEMS UPGRADE PACKAGE 1	
DRAWING TITLE:		PIPING AND INSTRUMENTATION DIAGRAM GAS GENERATOR LUBE OIL SYSTEM FOR 13-C-101A/B/102	
UNIT:	13	PLANT:	HABSHAN-1
CONTR. PROJ. No.:	AET01074.00	CONT. DWG. No.:	3143234
ADNOC GAS AGREEMENT No.:		4700018747	
ADNOC GAS PROJ. No.:	0405323	ADNOC GAS DWG. No.:	5323P1-H1-013-00-50-014
SHEET No.:		01/01	REV. No.:
14		15	SHEET SIZE

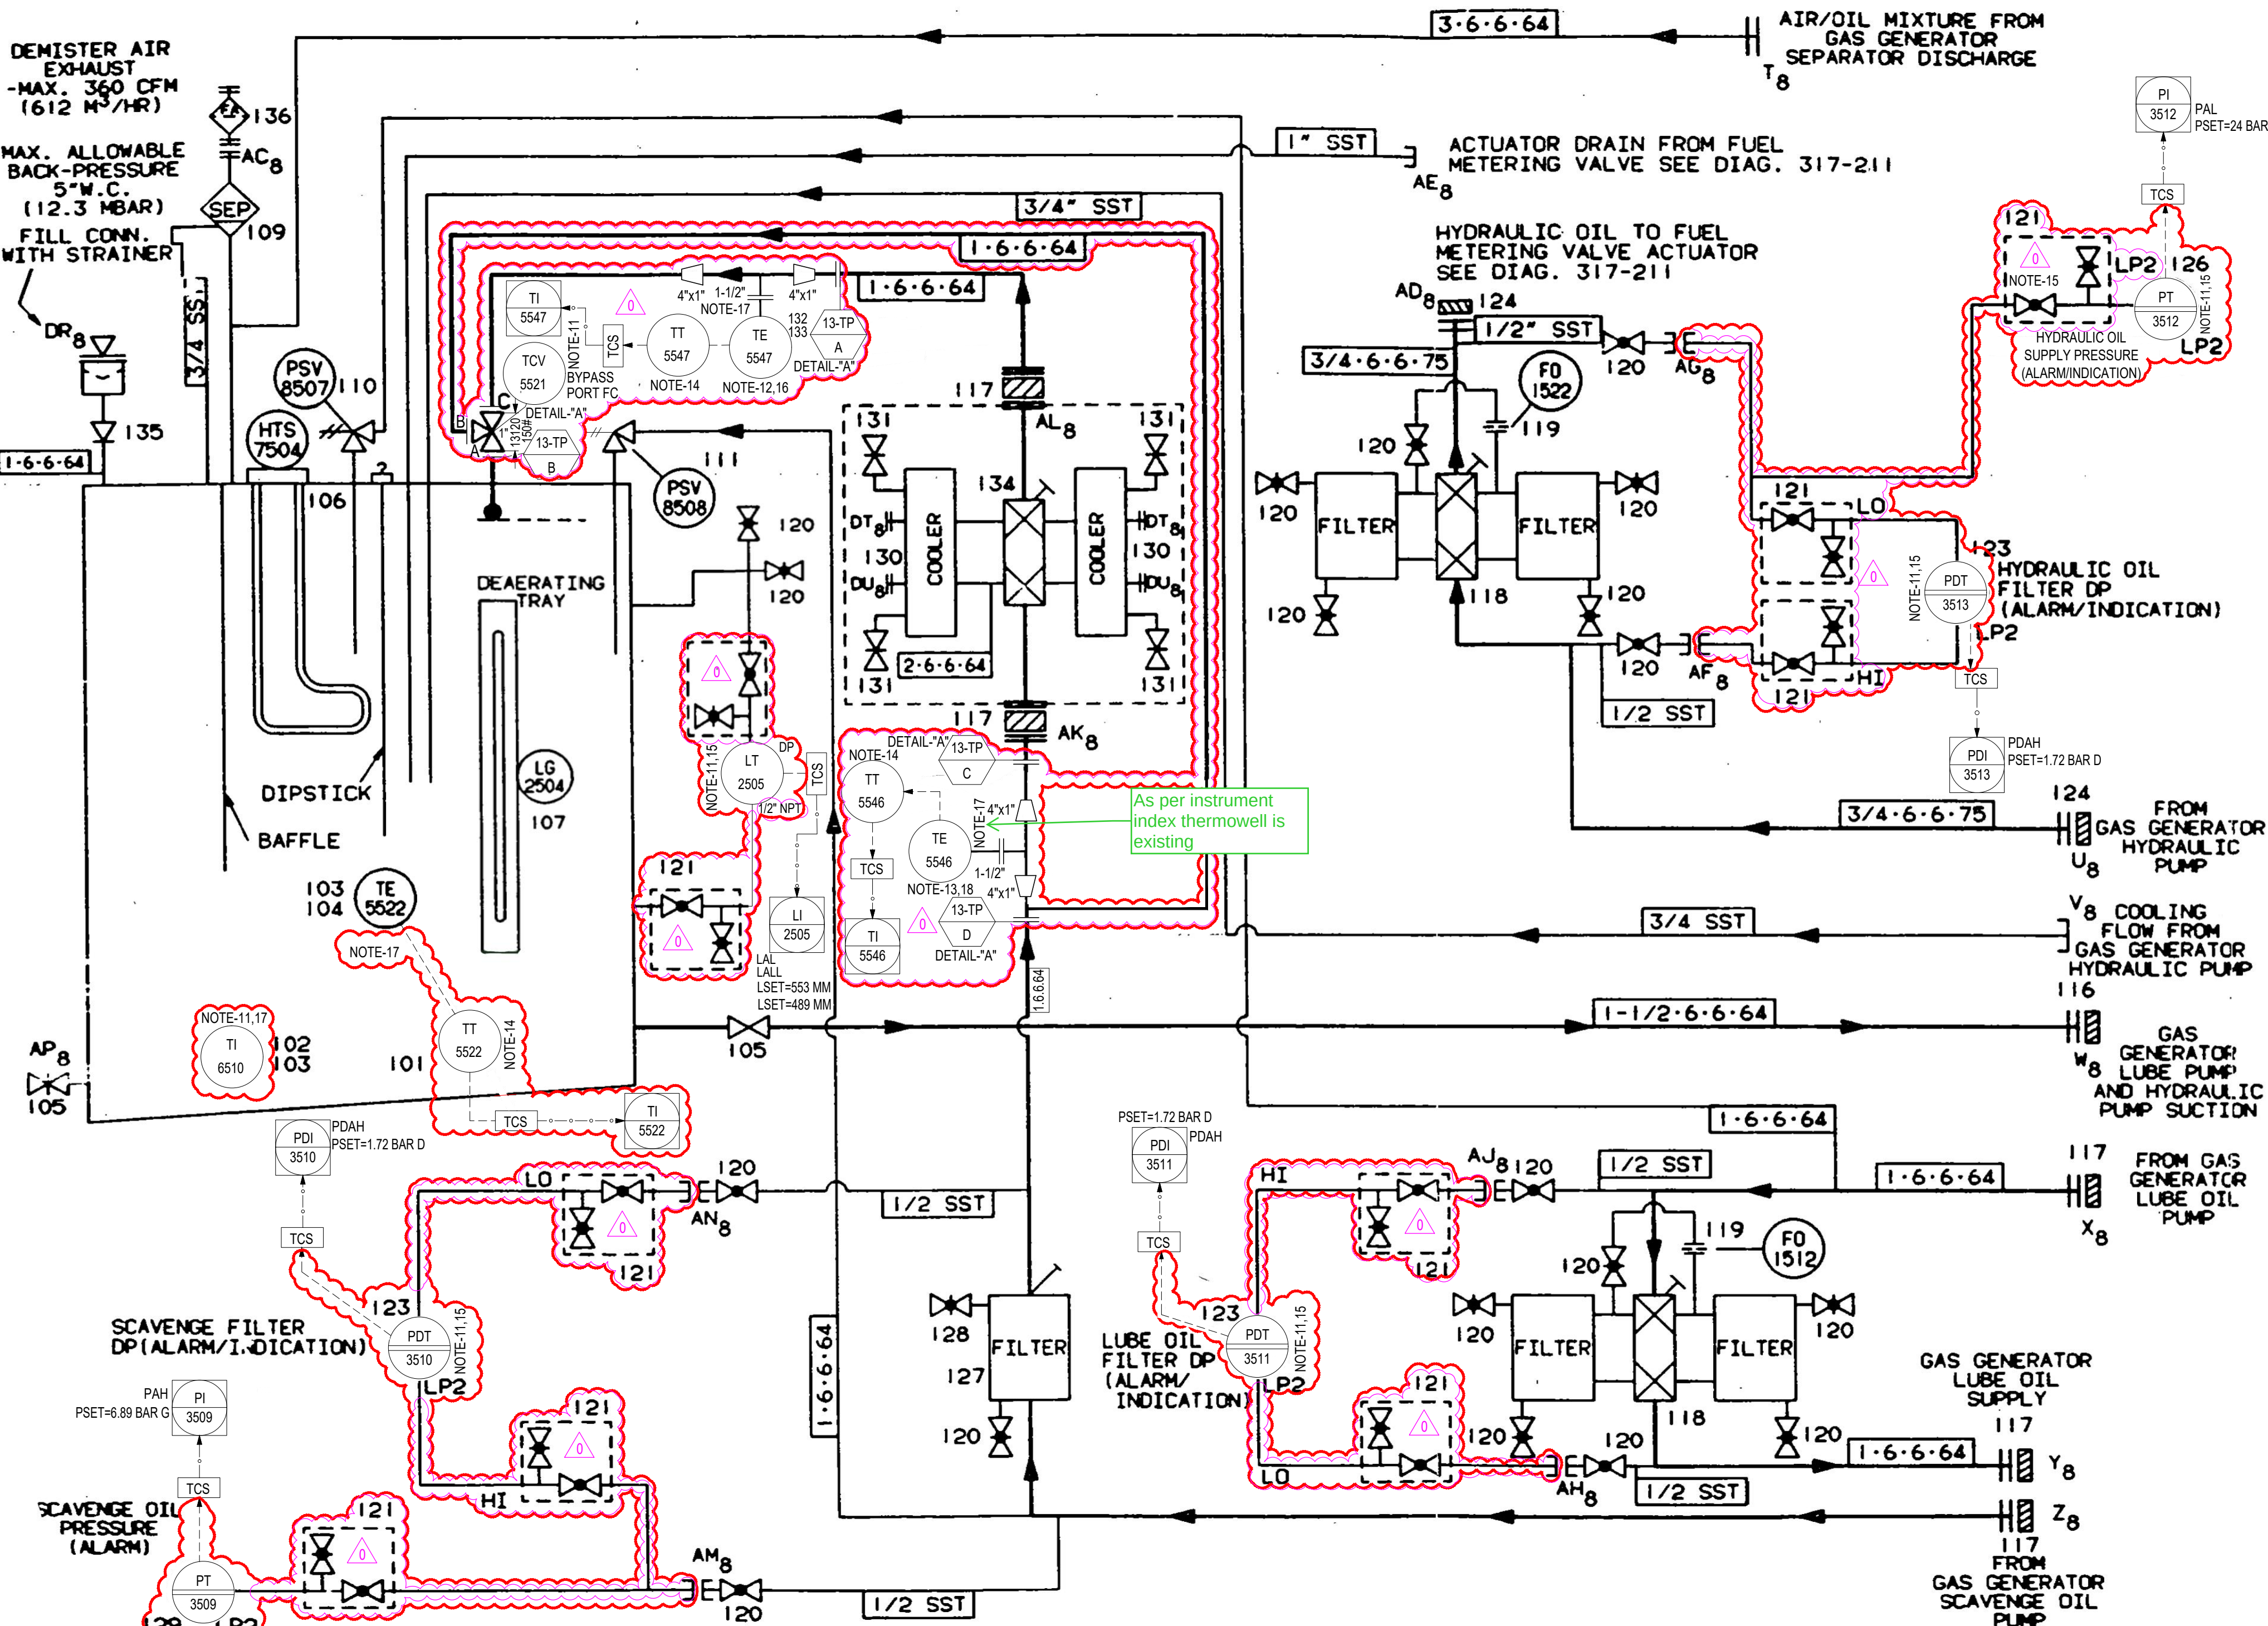

NOTE-21 DETAIL-"B"		
13-C-102	13-C-101A	13-C-101B
13-LT-2505	13-LT-2605	13-LT-2705
13-PDT-3510	13-PDT-3610	13-PDT-3710
13-PDT-3511	13-PDT-3611	13-PDT-3711
13-PDT-3513	13-PDT-3613	13-PDT-3713
13-PT-3509	13-PT-3609	13-PT-3709
13-PT-3512	13-PT-3612	13-PT-3712
13-TCV-5521	13-TCV-5621	13-TCV-5721
13-TE-5546	-	-
13-TE-5547	13-TE-5647	-
13-TI-6510	13-TI-6610	13-TI-6710
13-TT-5522	13-TT-5622	13-TT-5722
13-TT-5546	13-TT-5646	13-TT-5746
13-TT-5547	13-TT-5647	13-TT-5747
13-TW-5546	13-TW-5646	13-TW-5746
13-TW-5547	13-TW-5647	13-TW-5747

DETAIL-"A"		
PACKAGE	INSTRUMENT TAG	TIE-IN NO.
13-C-102	13-TCV-5521	13-TP-841 A/B/C/D
13-C-101A	13-TCV-5621	13-TP-4023 A/B/C/D
13-C-101B	13-TCV-5721	13-TP-4024 A/B/C/D

CONTRACT NO. 21712800	BY	DATE	DR-61 GAS GENERATOR OIL CONSOLE DIAGRAM
TYPE DRG 12	DRAWN	DLM 07/16/92	
SCALE NONE	CHECKED	JJM 07/17/92	
DEPT. 63.81	REDRAW		
DRAFTING APPROVAL	D.J.L	07/17/92	
CONTRACT APPROVAL	JAB	07/17/92	
SYSTEM APPROVAL	JJM	07/17/92	
ADNOC GAS AGREEMENT No.:			
ADNOC GAS PROJ. No.:			
ADNOC GAS DWS. No.:			
317-210	SHT.	REV.	03
LICENSEE			